


จุดตรวจพื้นที่ ITC 2

ZONE 1-13

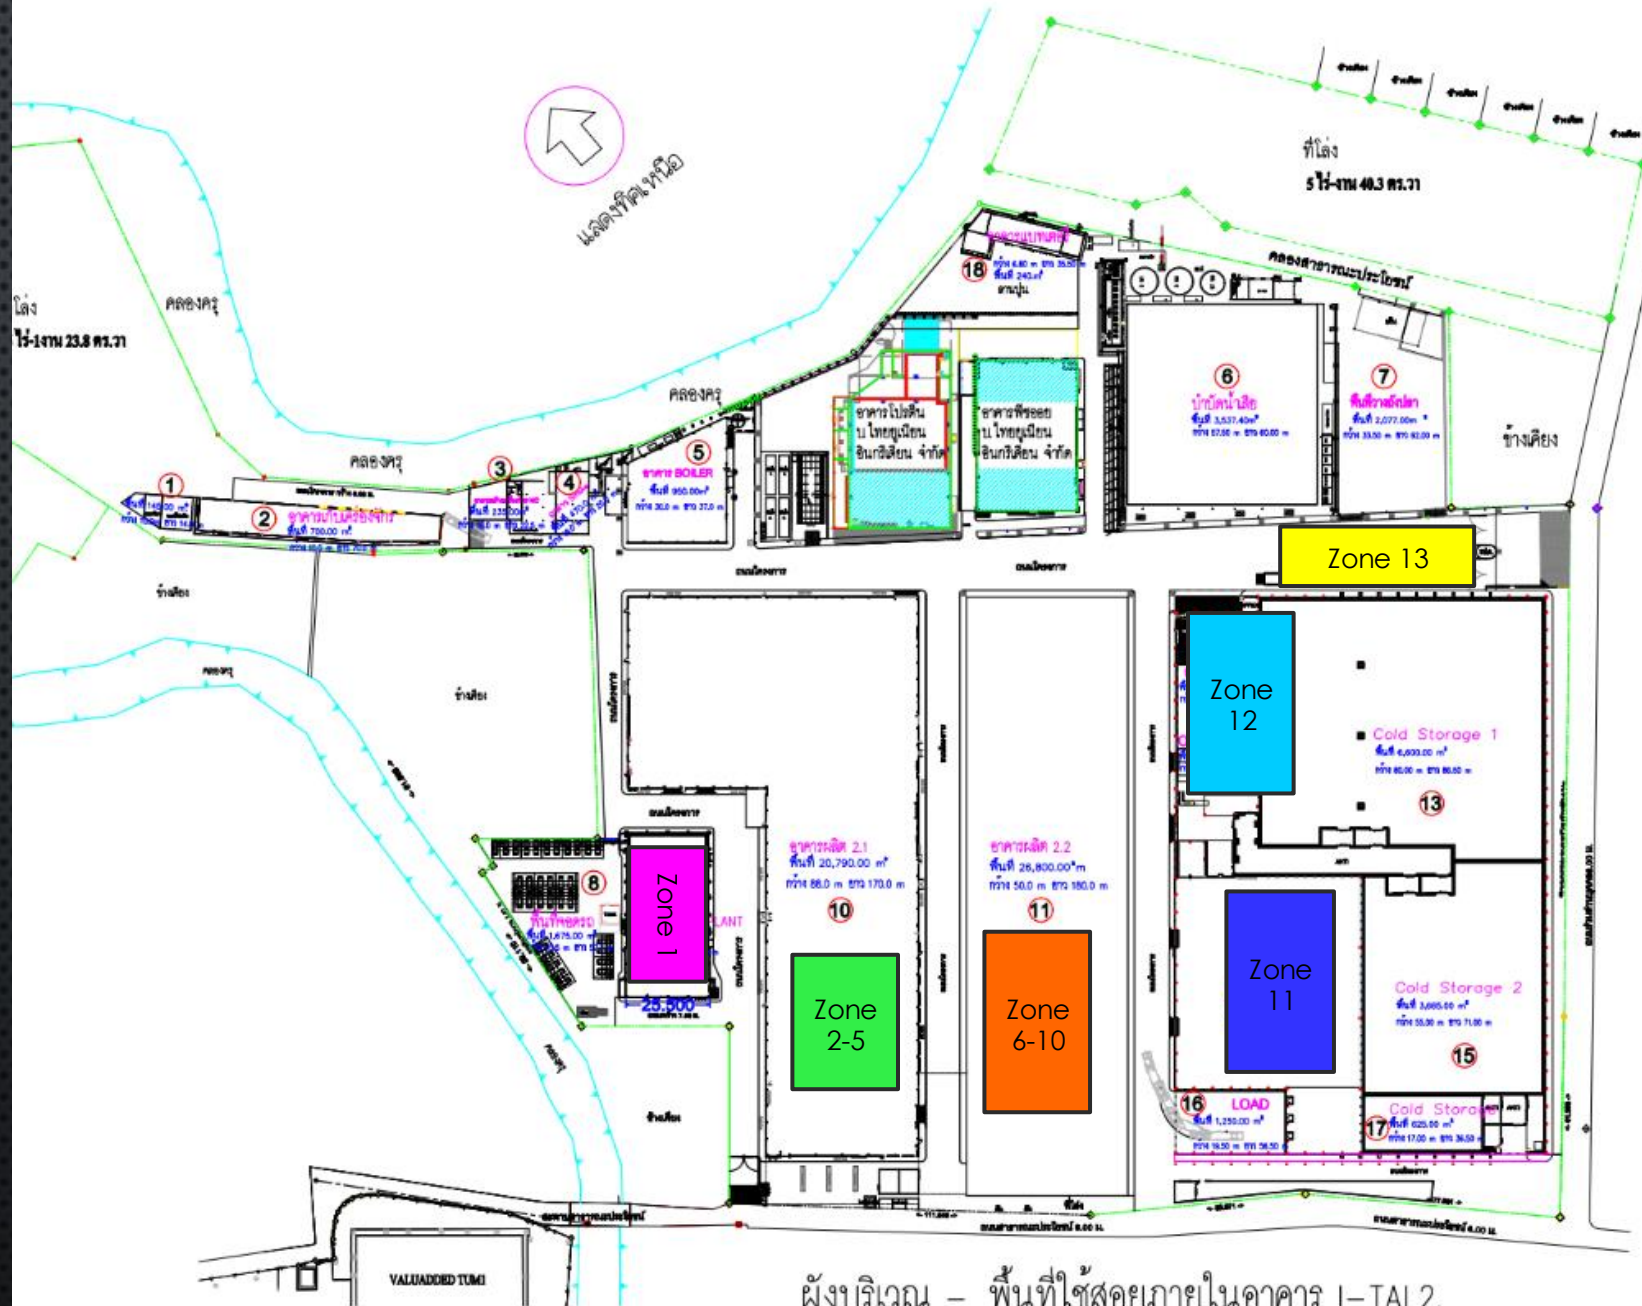

ผังบริเวณ - พื้นที่ใช้สอยภายในอาคาร I-TAL2.

มาตราส่วน 1:2000

ZONE 1

PILOT PLANT



Zone 1 Pilot Plant F5


Office


Meeting

ห้องน้ำ

ห้องครัว

ห้อง Lab

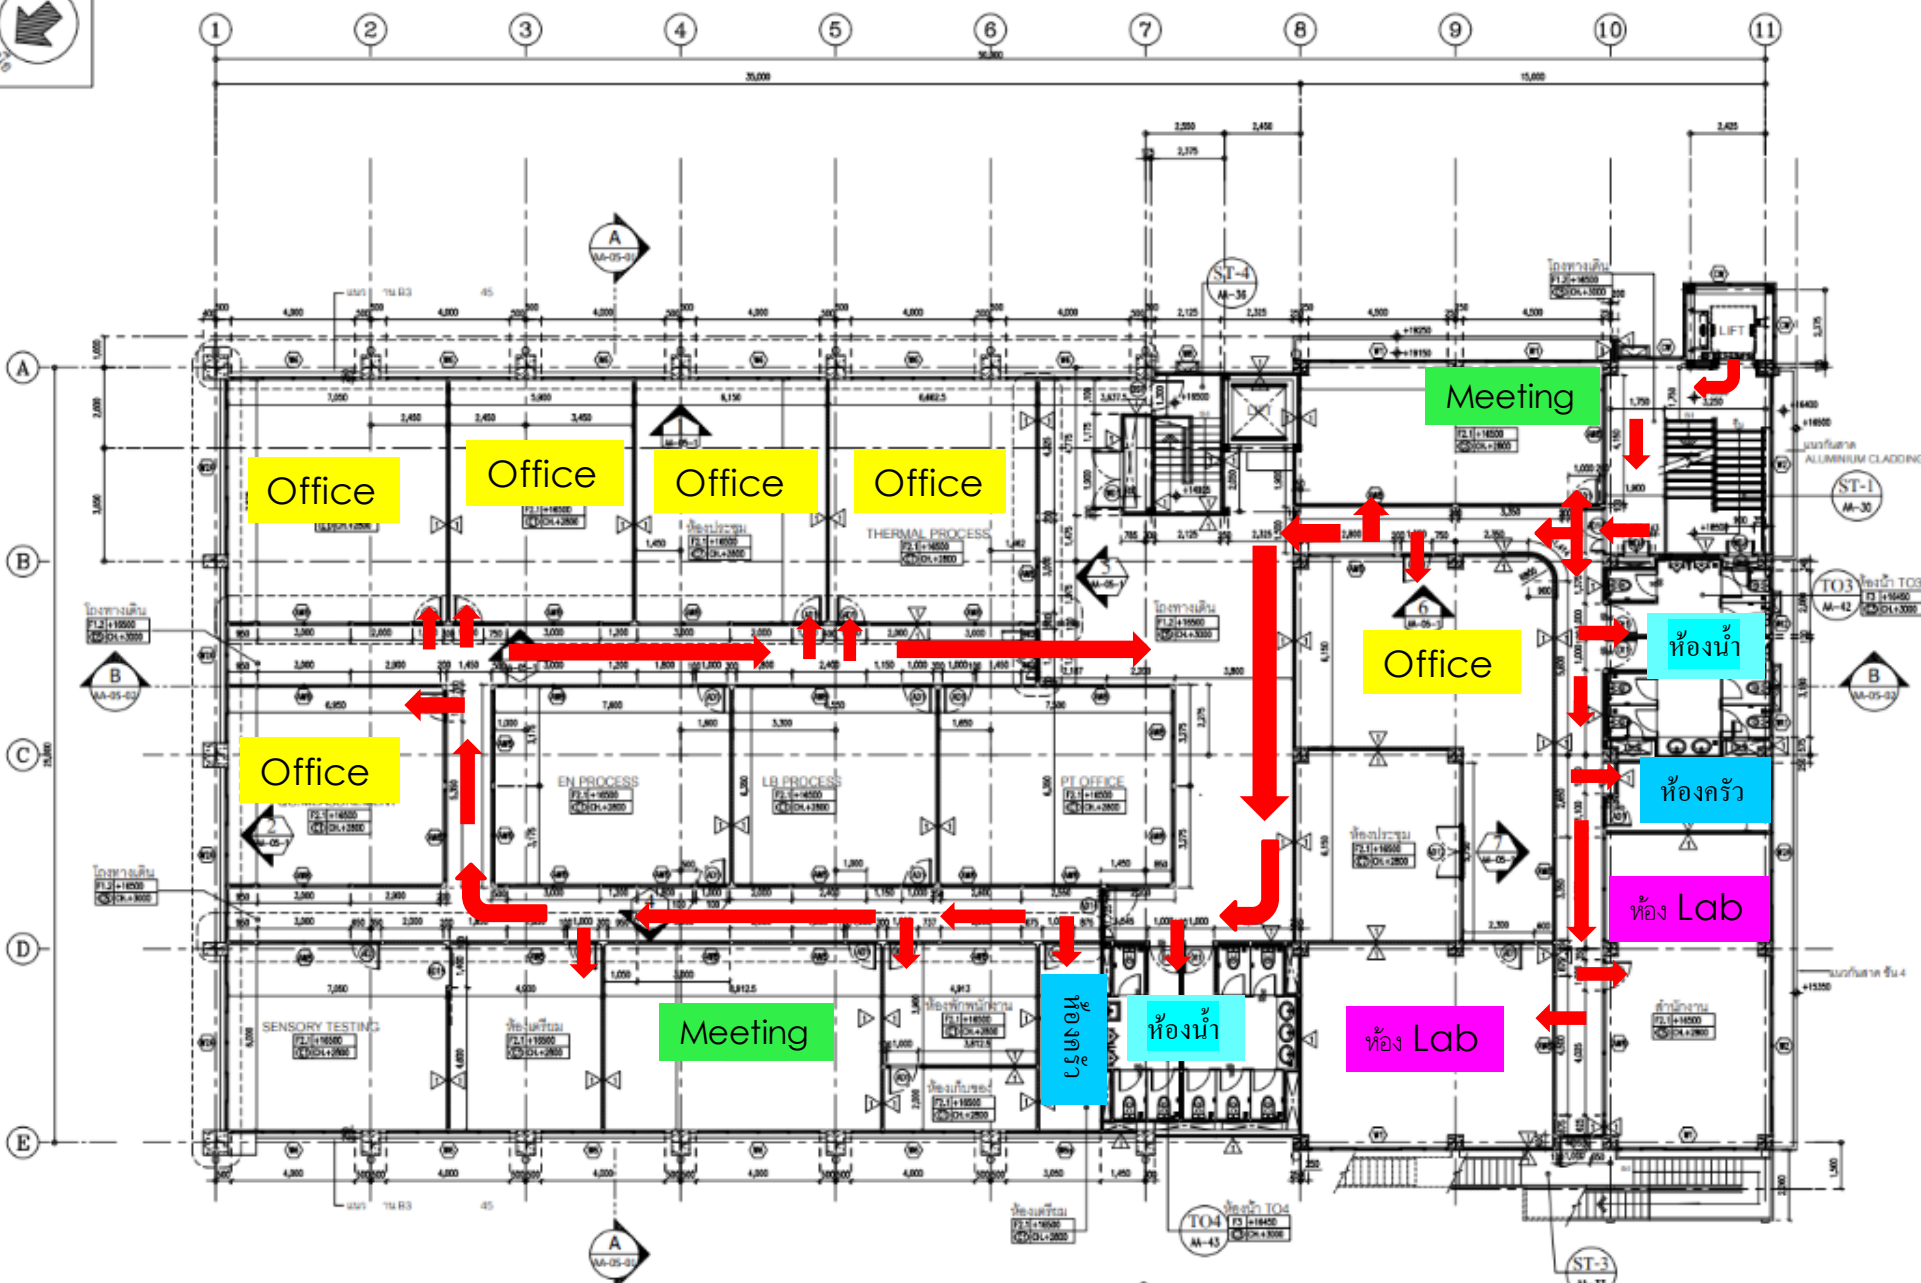

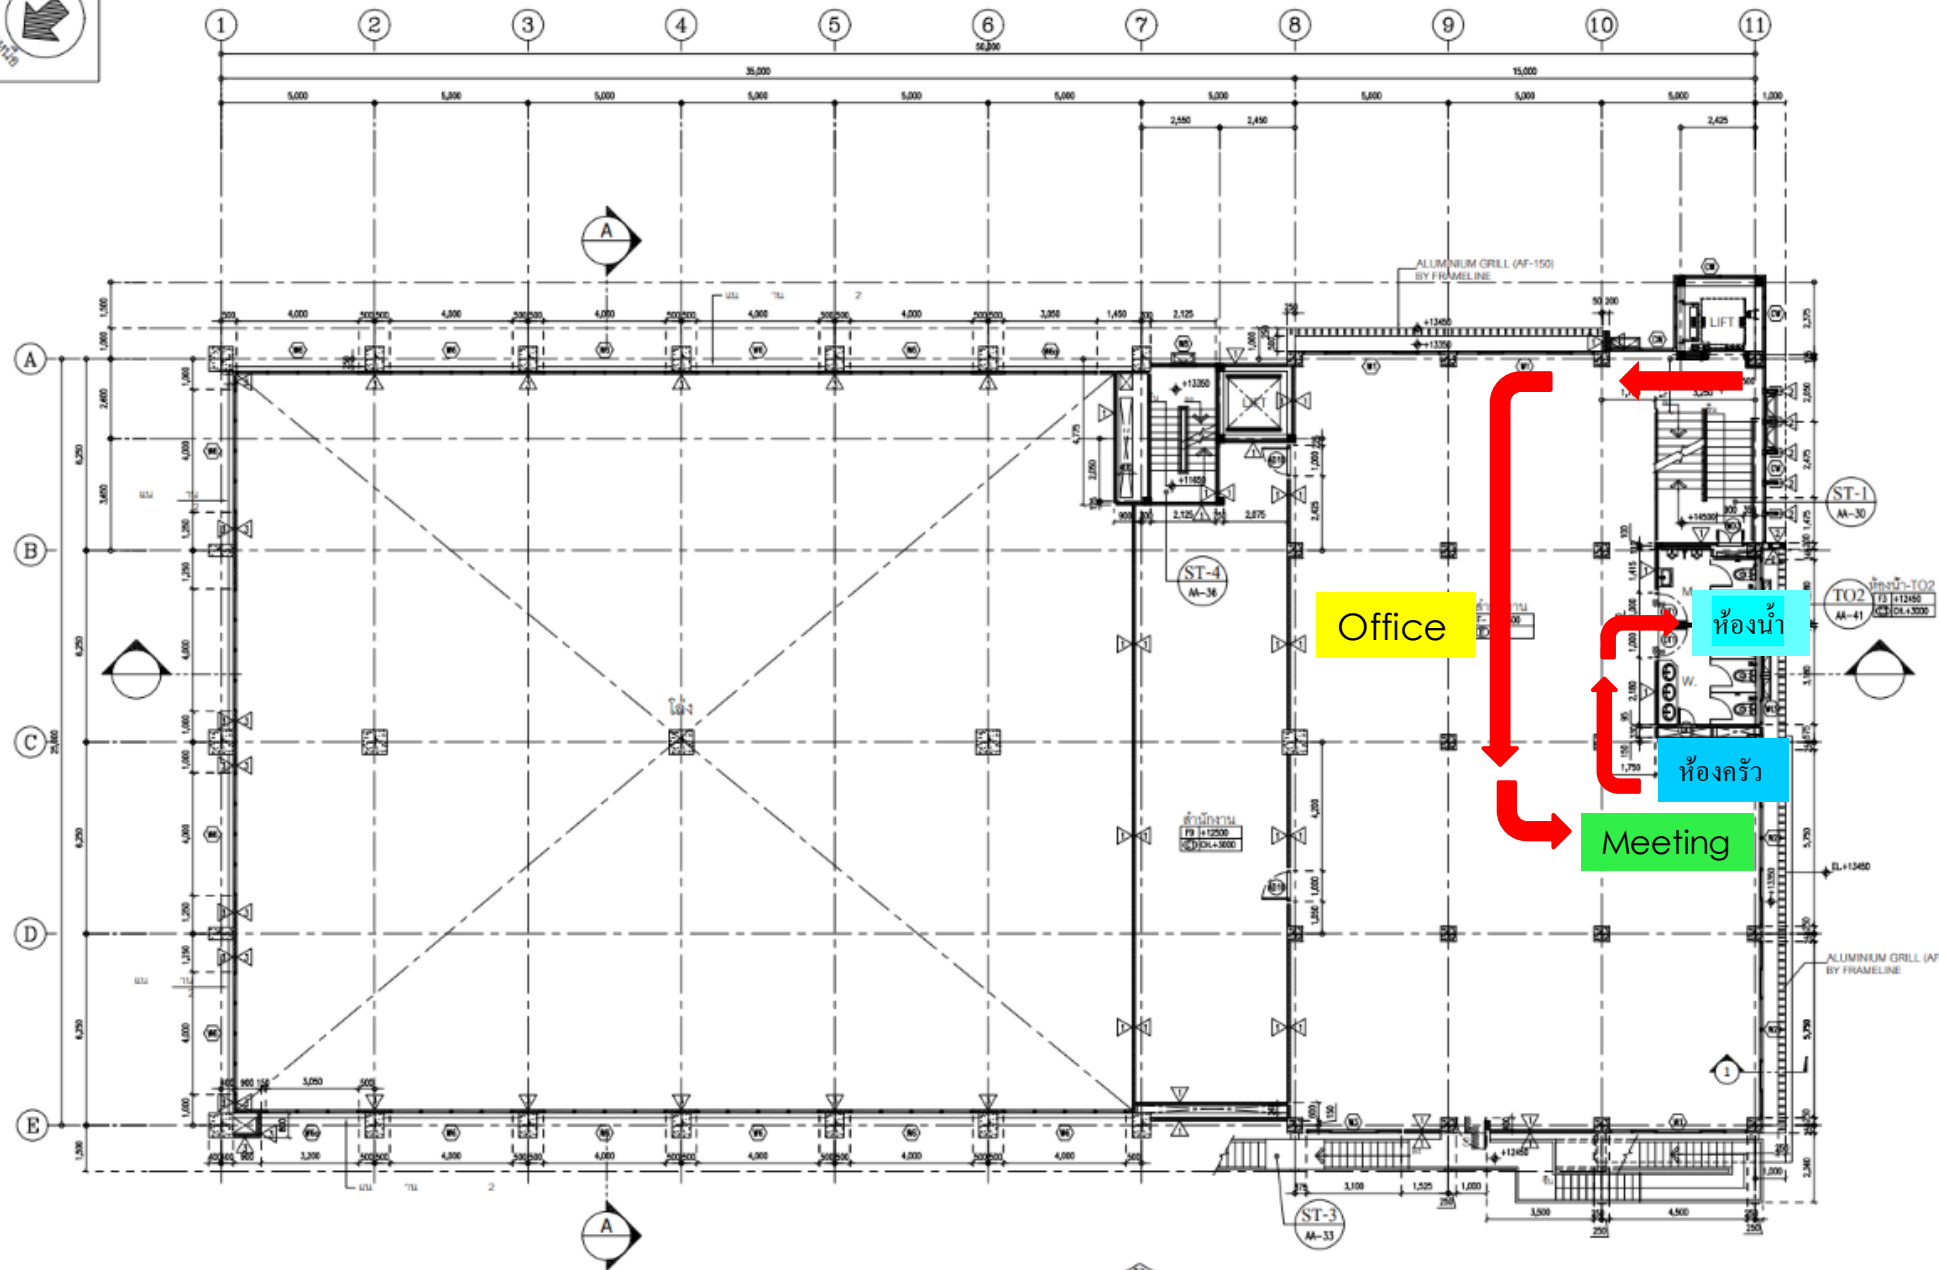

แปลนพื้นที่ 4
A1 SCALE 1:100
A3 SCALE 1:200



Zone 1 Pilot Plant F4

Office

Meeting

ห้องน้ำ

ห้องครัว

Office

ห้องน้ำ

ห้องครัว

Meeting



Zone 1 Pilot Plant F3

Office


ห้อง Lab

ห้องน้ำ

ห้องครัว

ห้อง Lab

ห้องเก็บอุปกรณ์

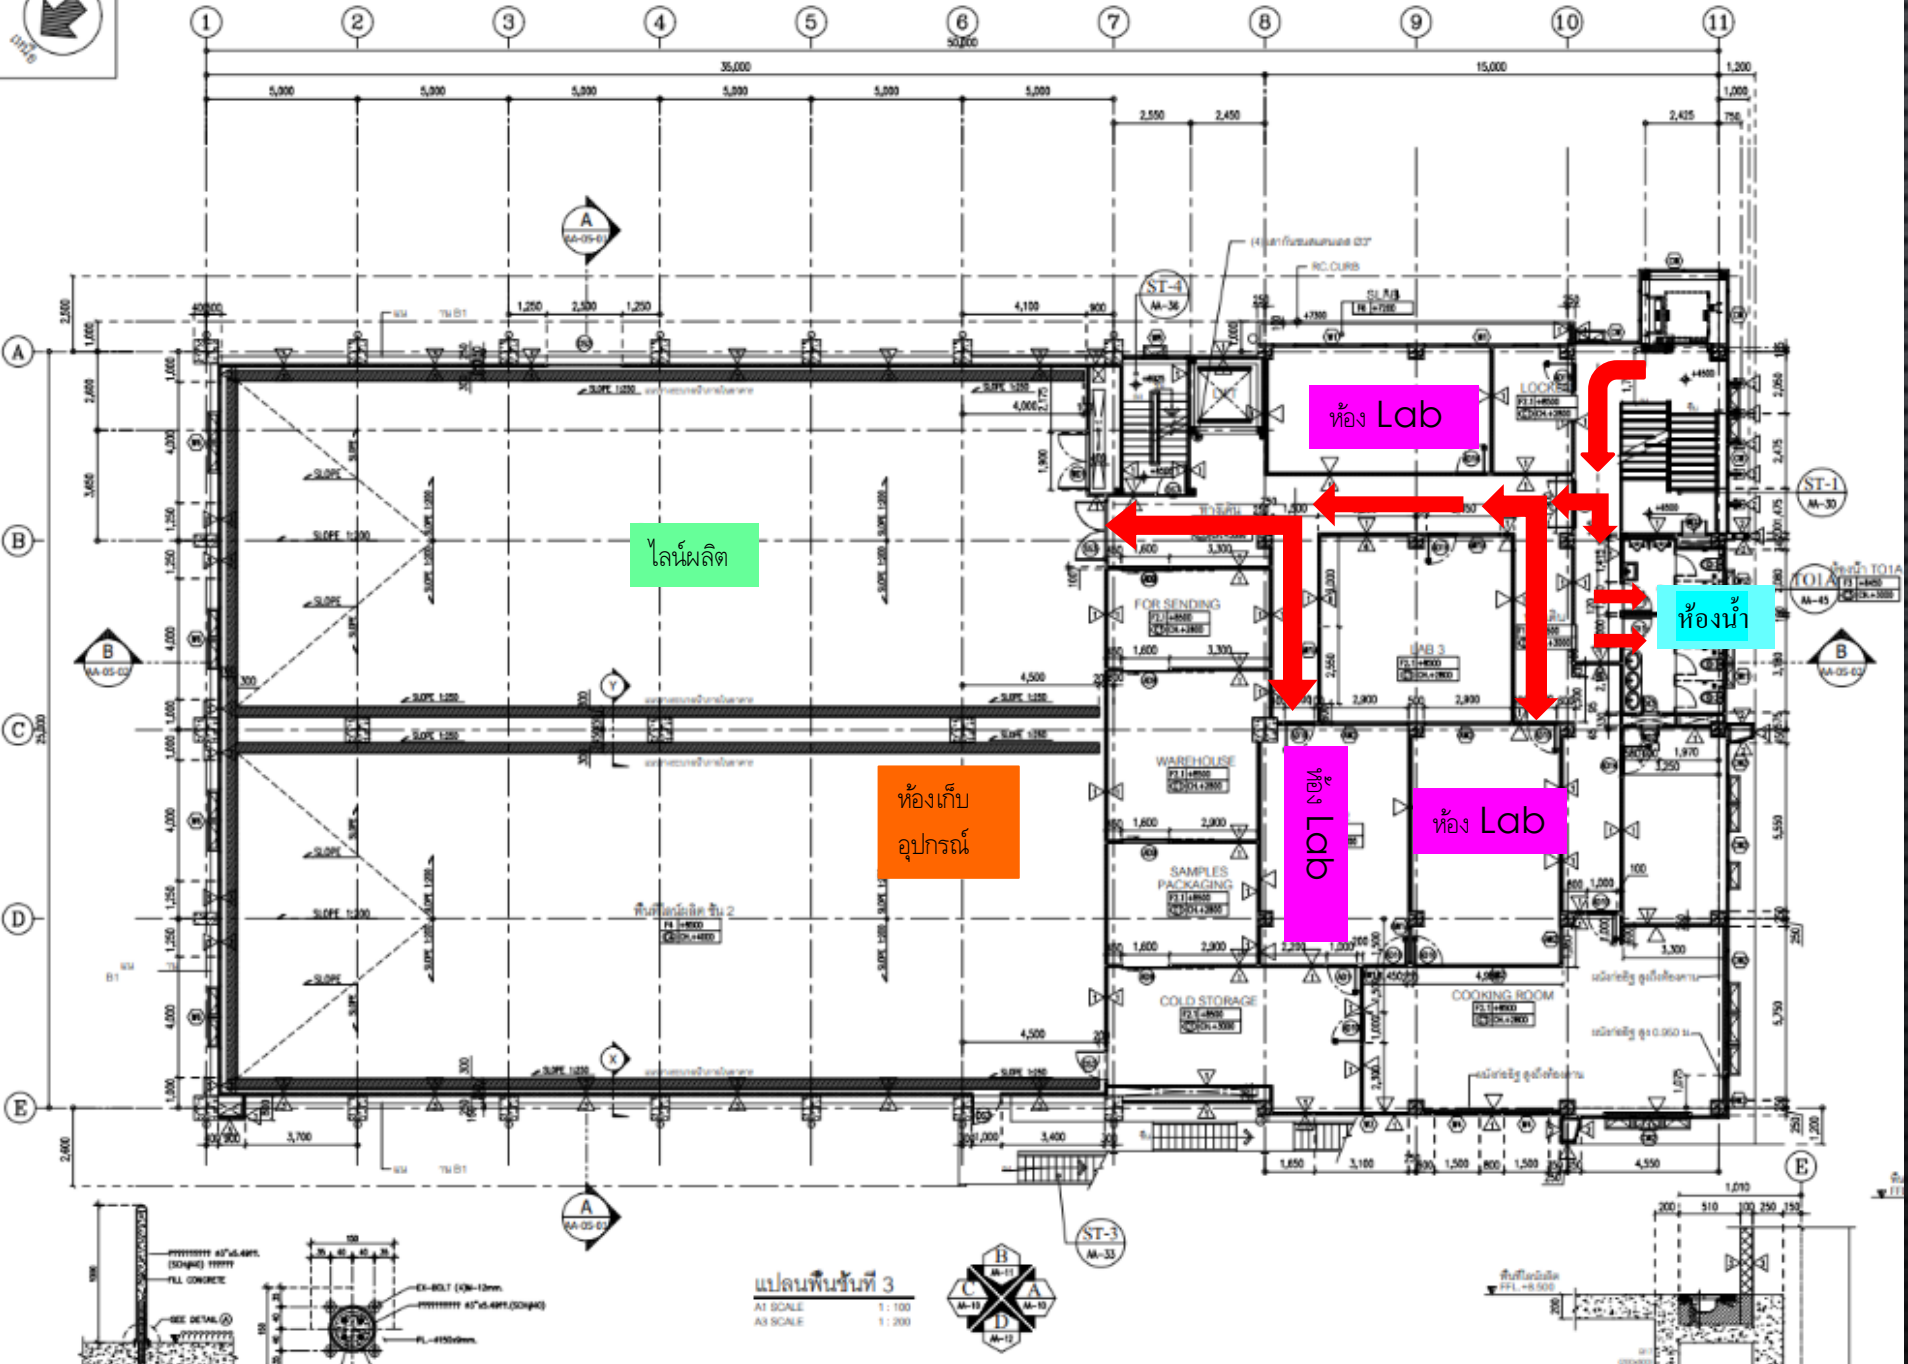

แปลนพื้นที่ 3
A1 SCALE 1:100
A3 SCALE 1:200







Zone 1 Pilot Plant F2

Meeting

ห้องน้ำ

ห้องครัว

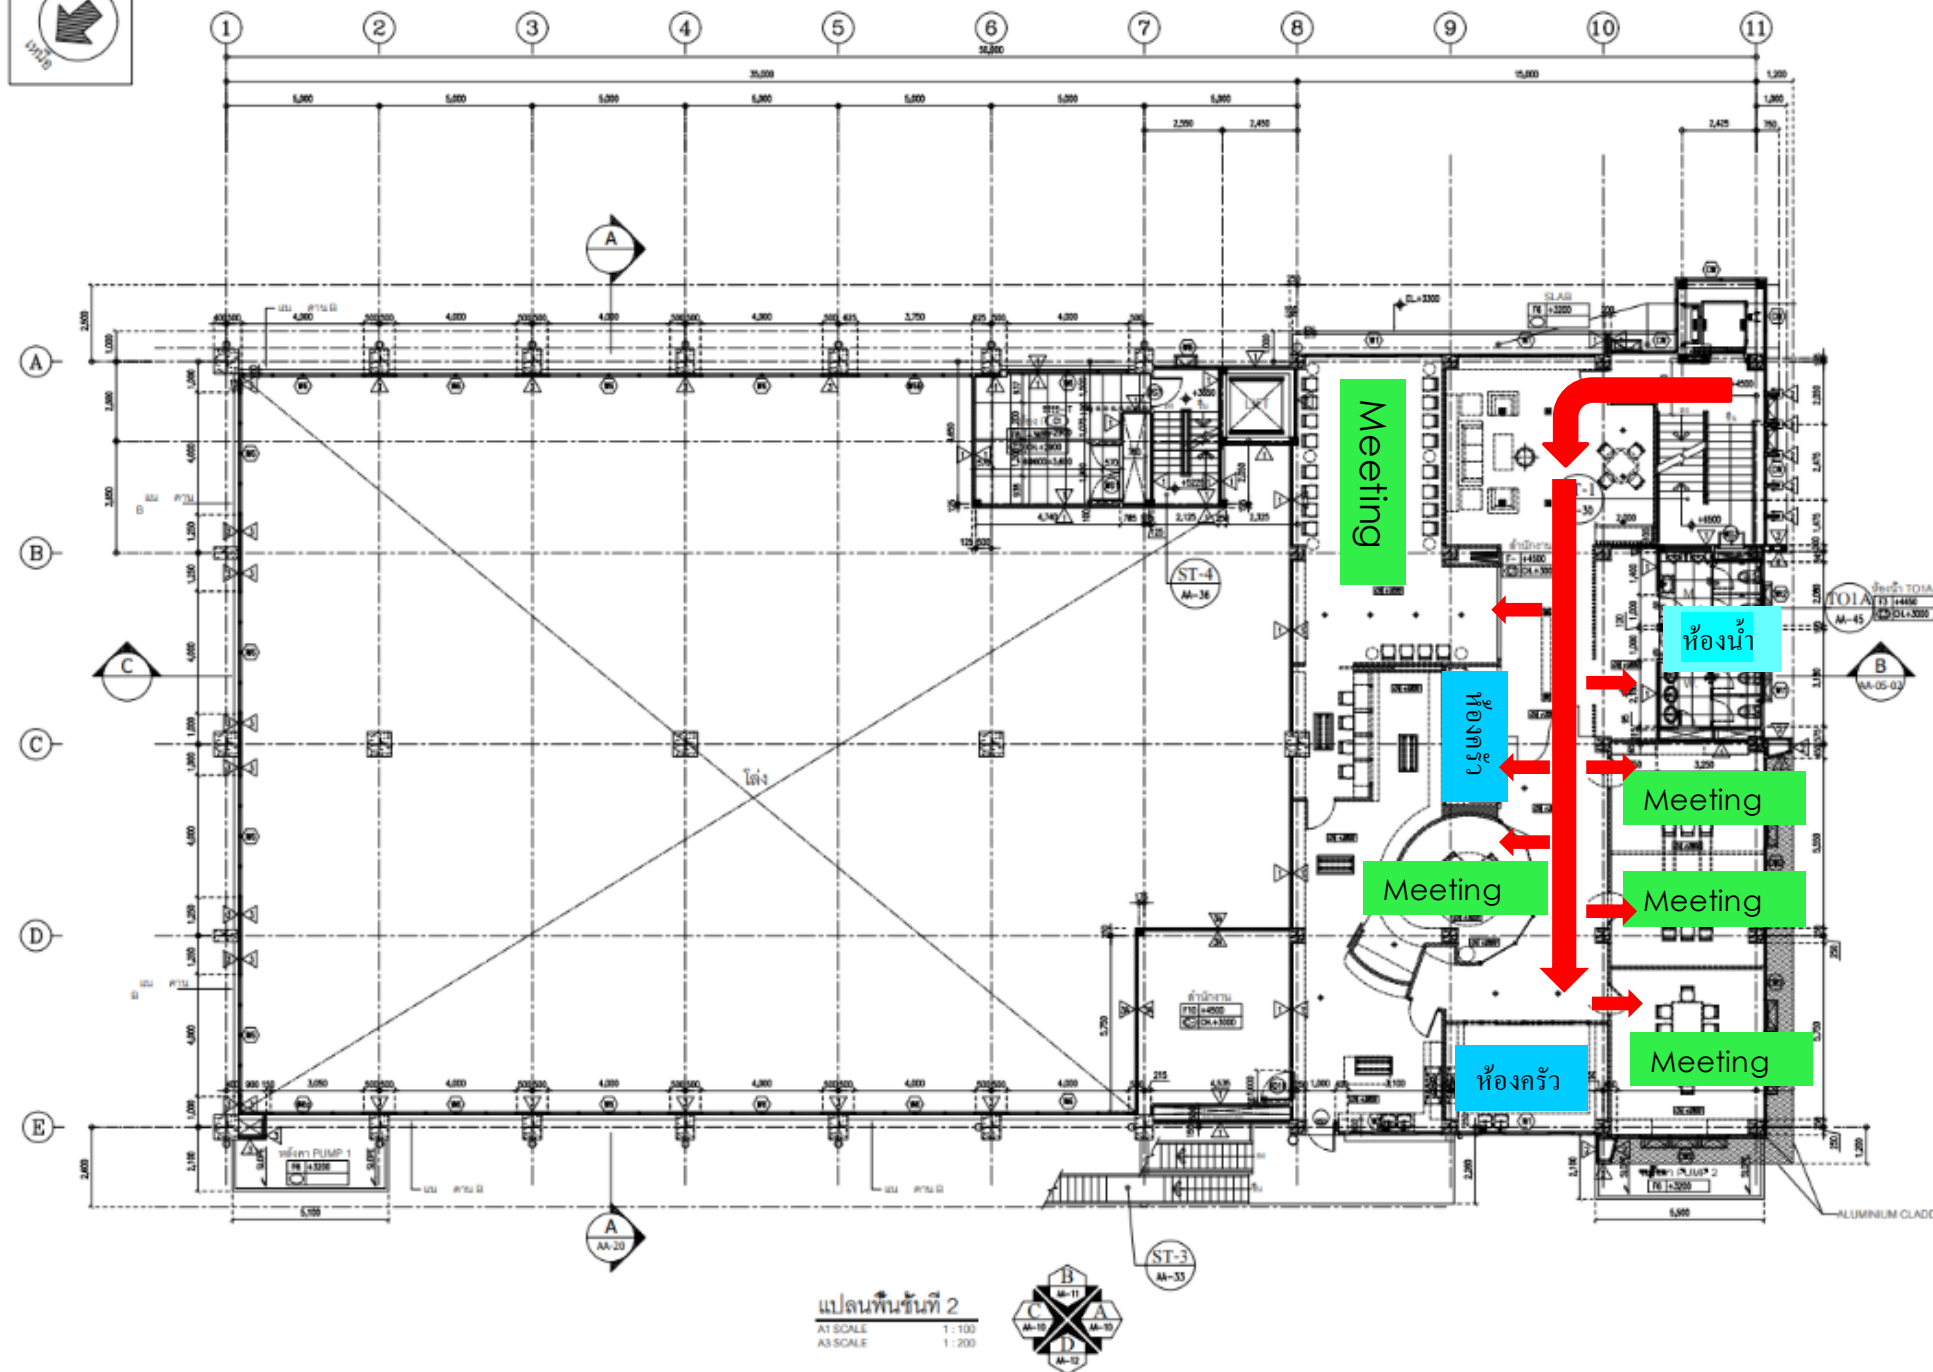

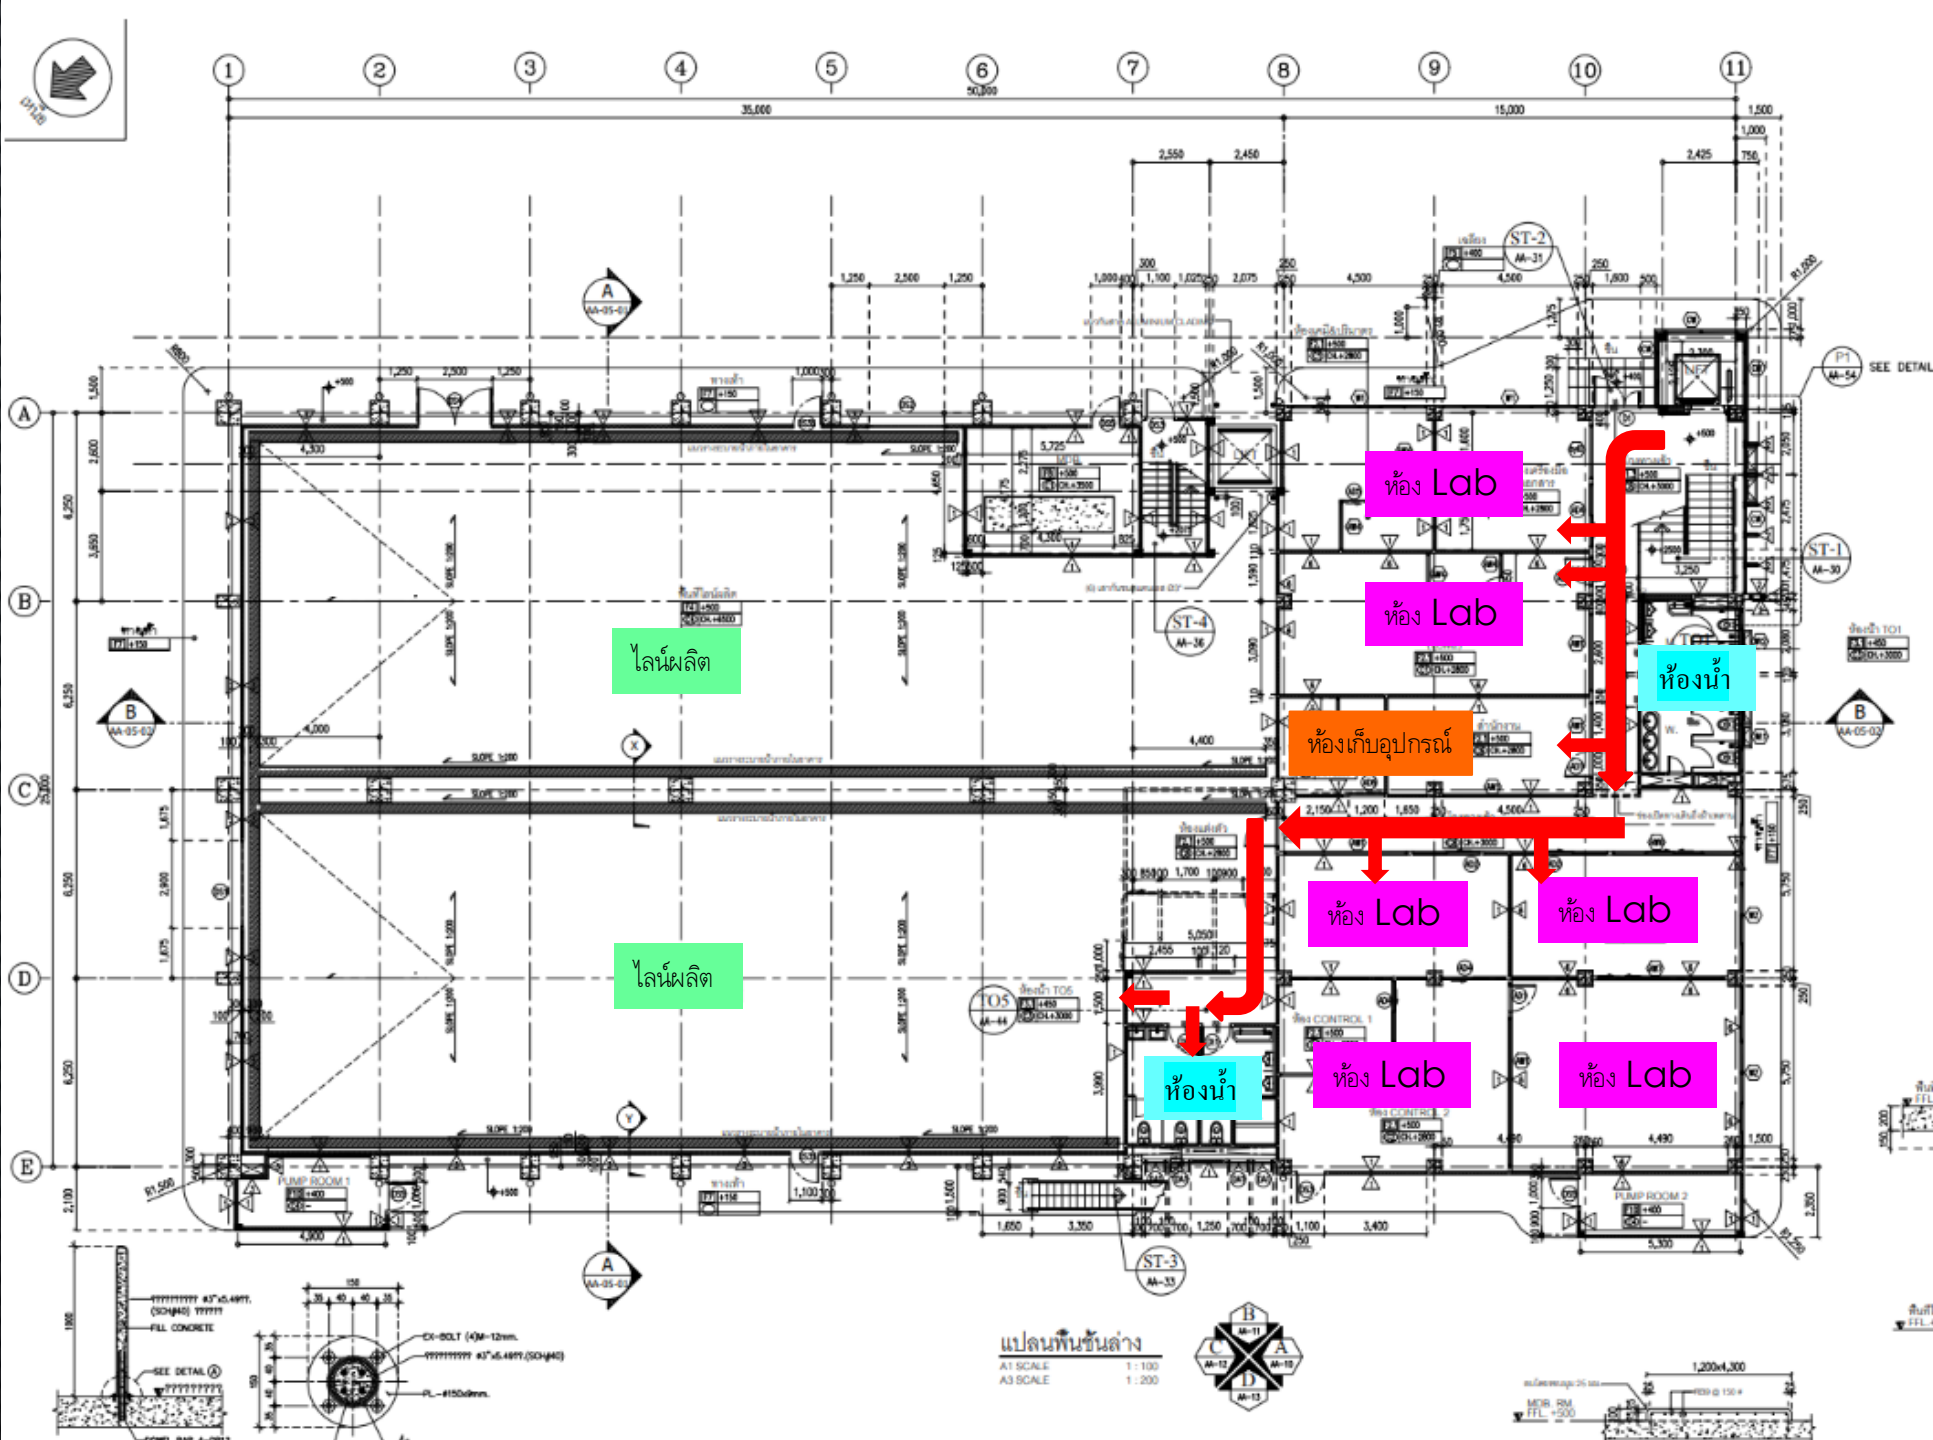

Zone 1 Pilot Plant F1

Meeting

ห้องน้ำ

ห้อง Lab

ไลน์ผลิต


ห้องเก็บอุปกรณ์

ZONE 2

OFFICE ITC 2.1 F2


Zone 1 Office
ITC 2.1 F2

- Office
- Meeting
- ห้องน้ำ
- ห้องครัว
- ห้อง Lab

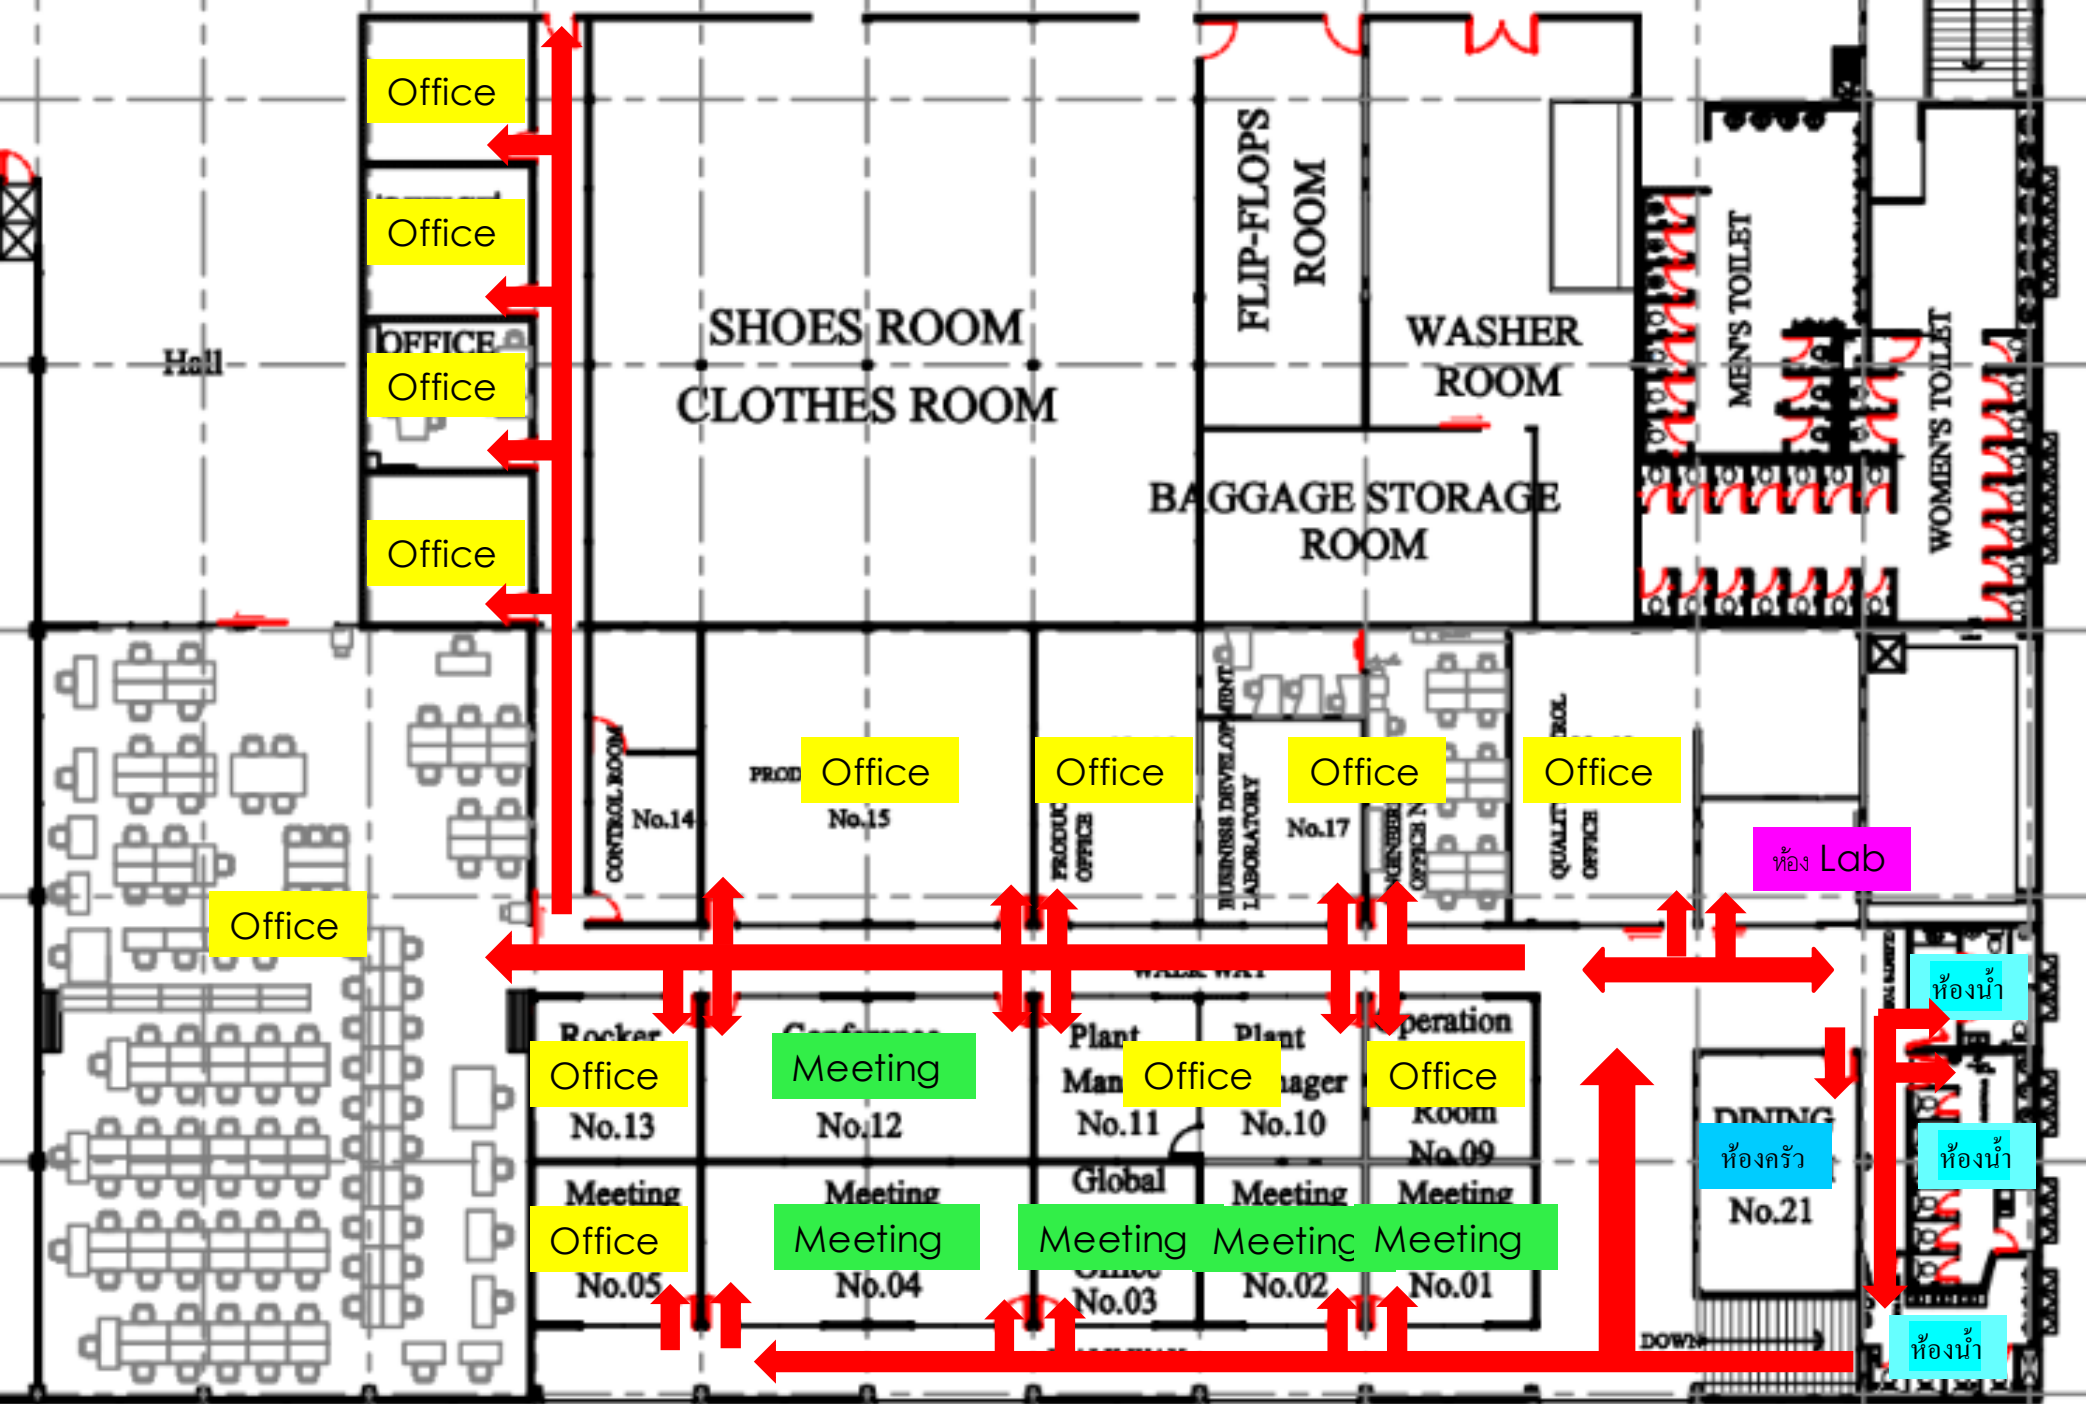

ZONE 3

พื้นที่ส่วนกลาง ITC 2.1 F2

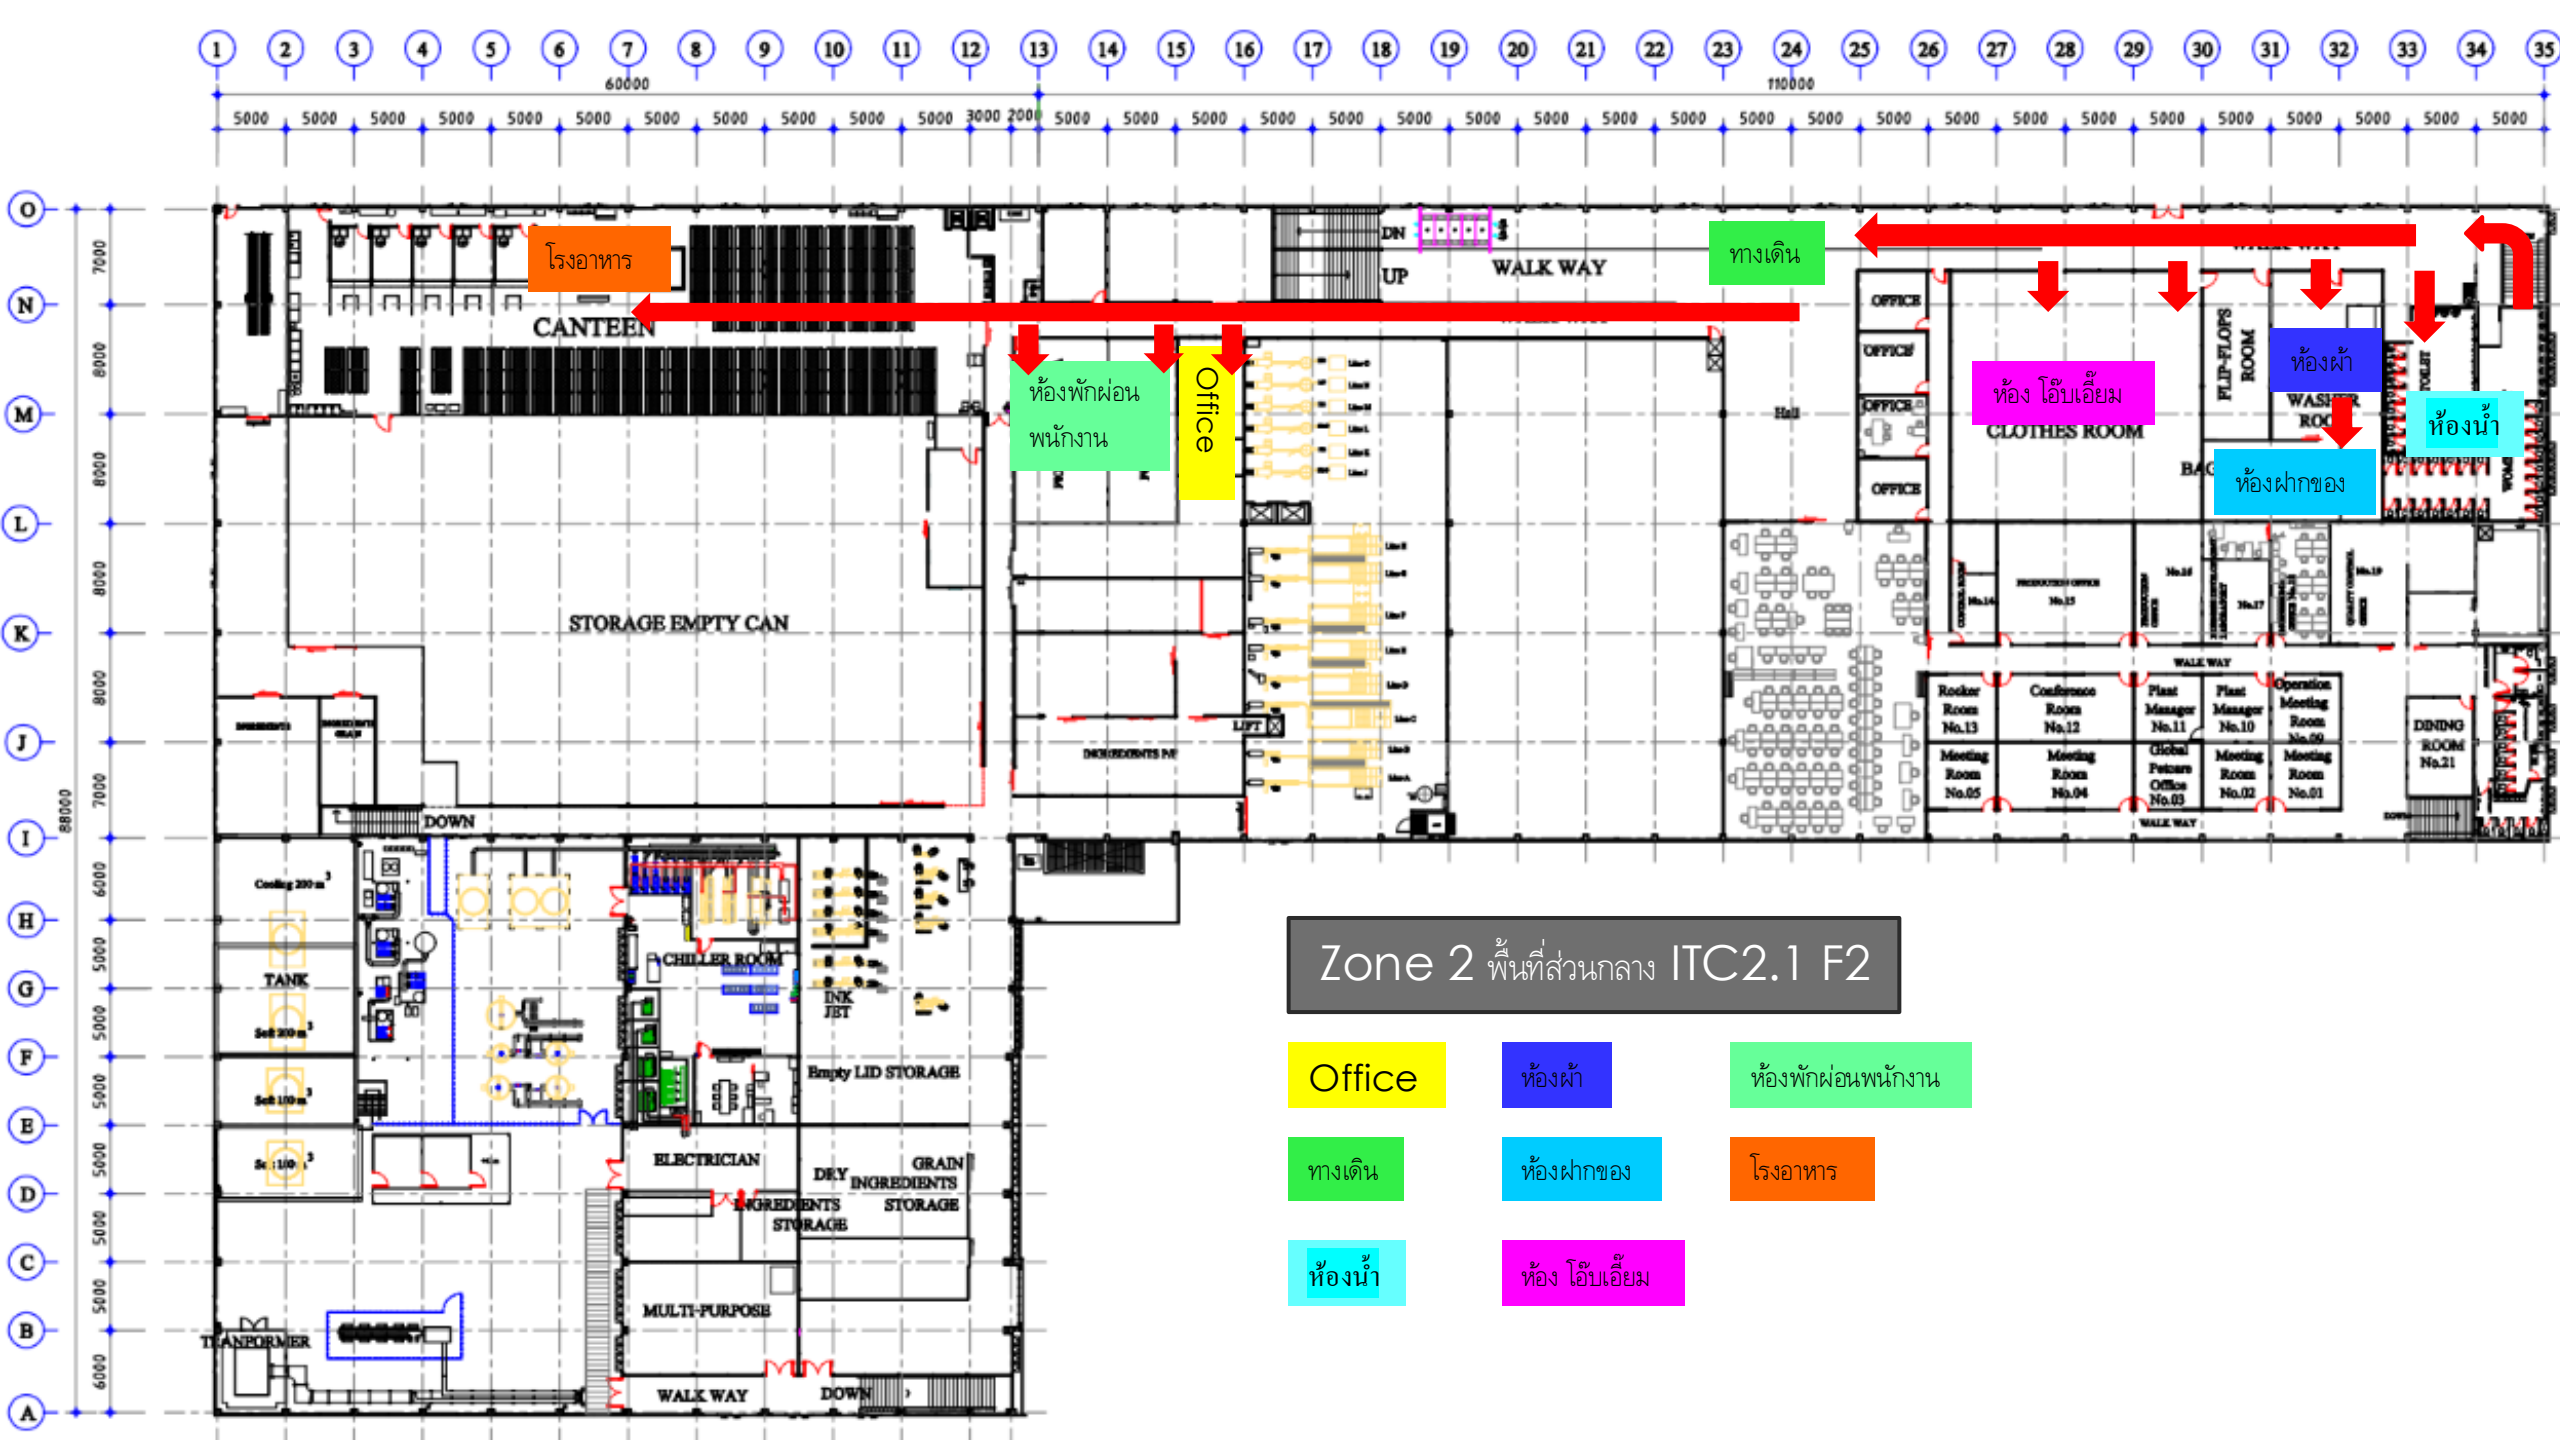

ZONE 4

พื้นที่การผลิต ITC 2.1 F2

Zone 4 พื้นที่การผลิต ITC2.1 F2


ห้องชำระ

สโตร์

ห้องINK

ห้องปล่อยกระป๋อง

ข้อป้างด้านหลัง

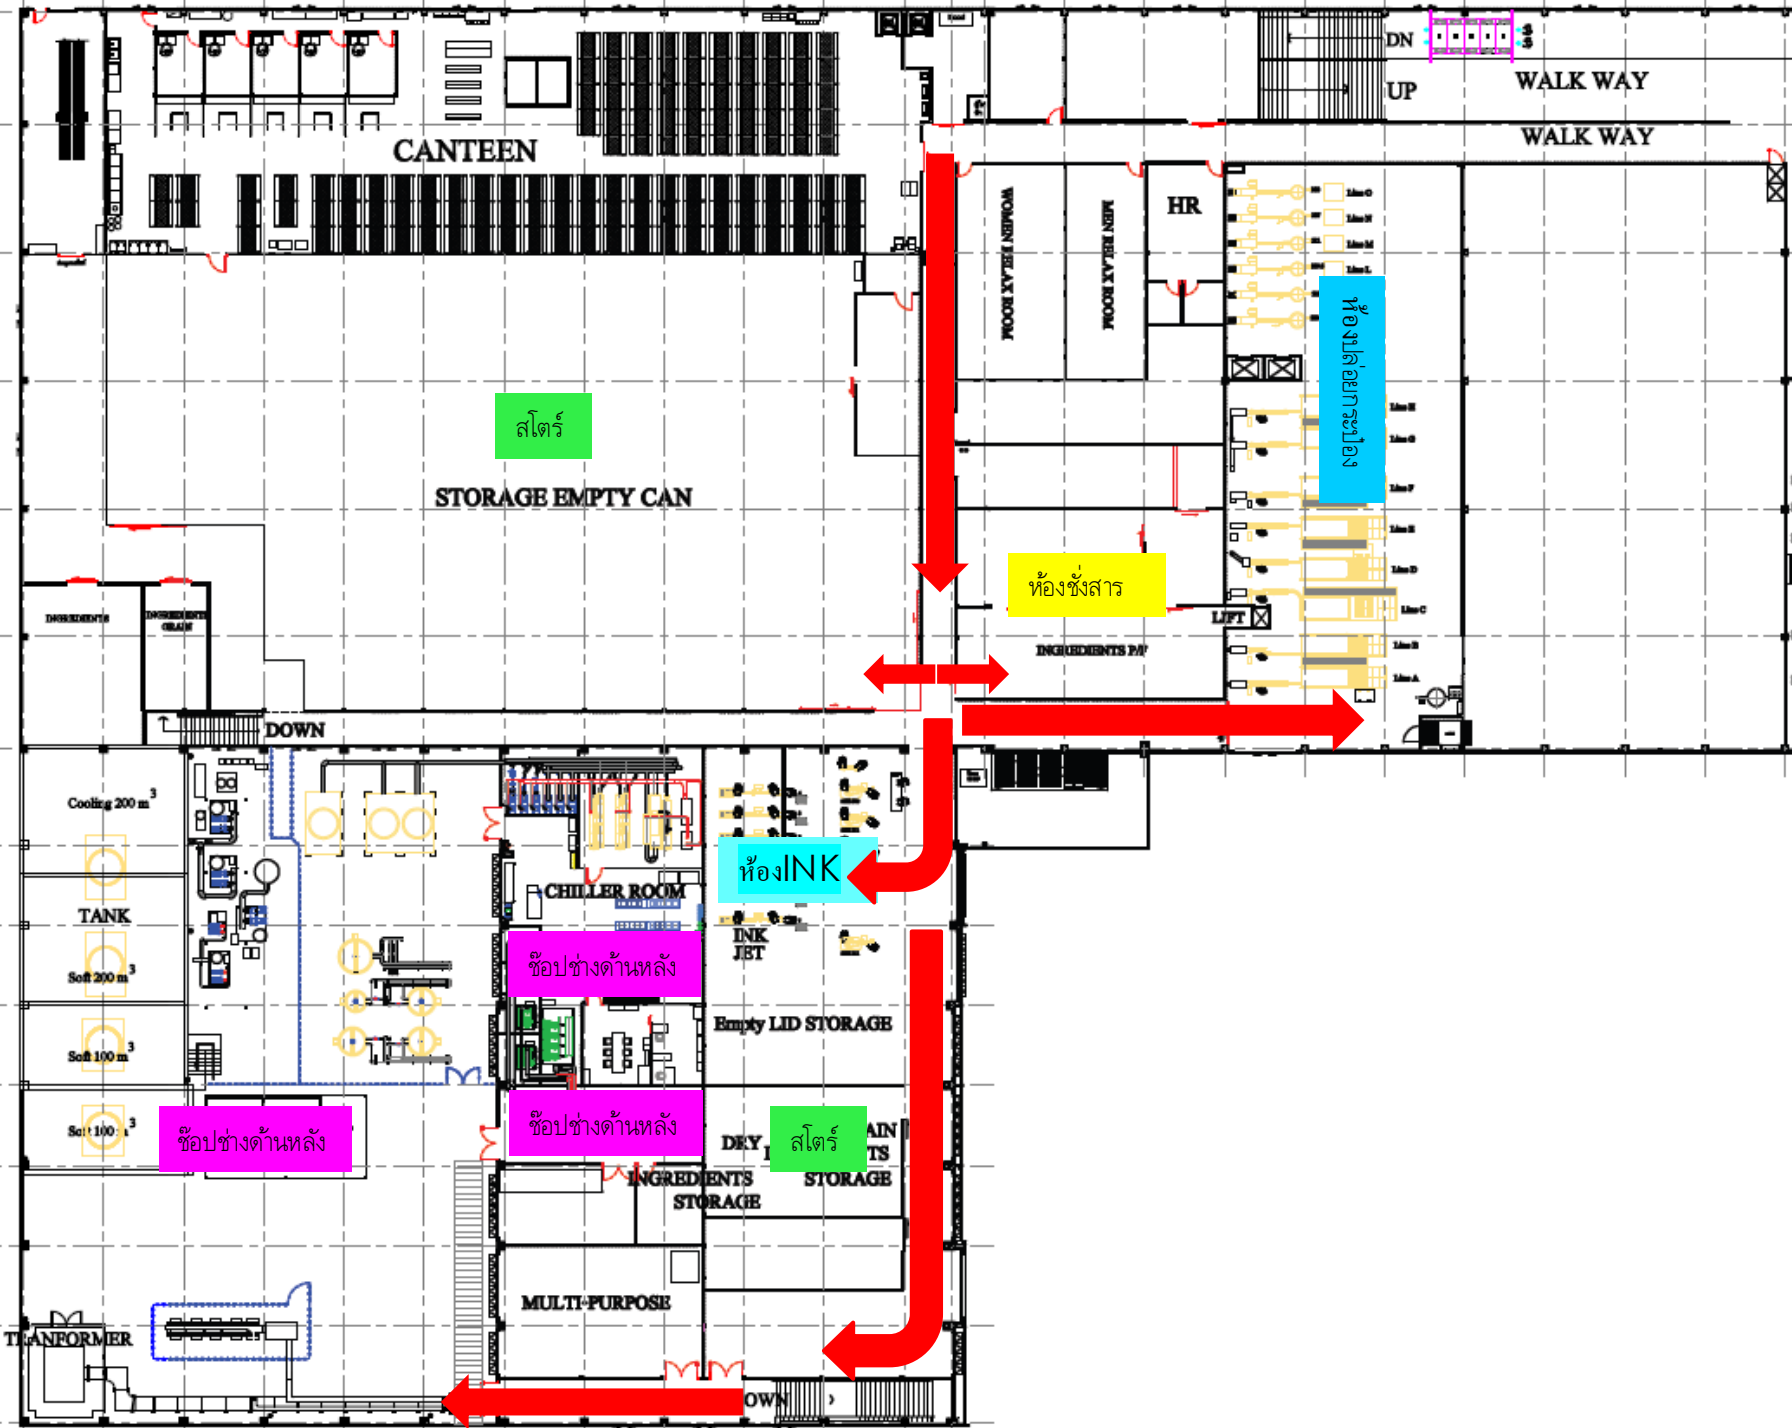


ZONE 5

พื้นที่การผลิต ITC 2.1 F1

ZONE 6

พื้นที่การผลิต ITC 2.2 F1

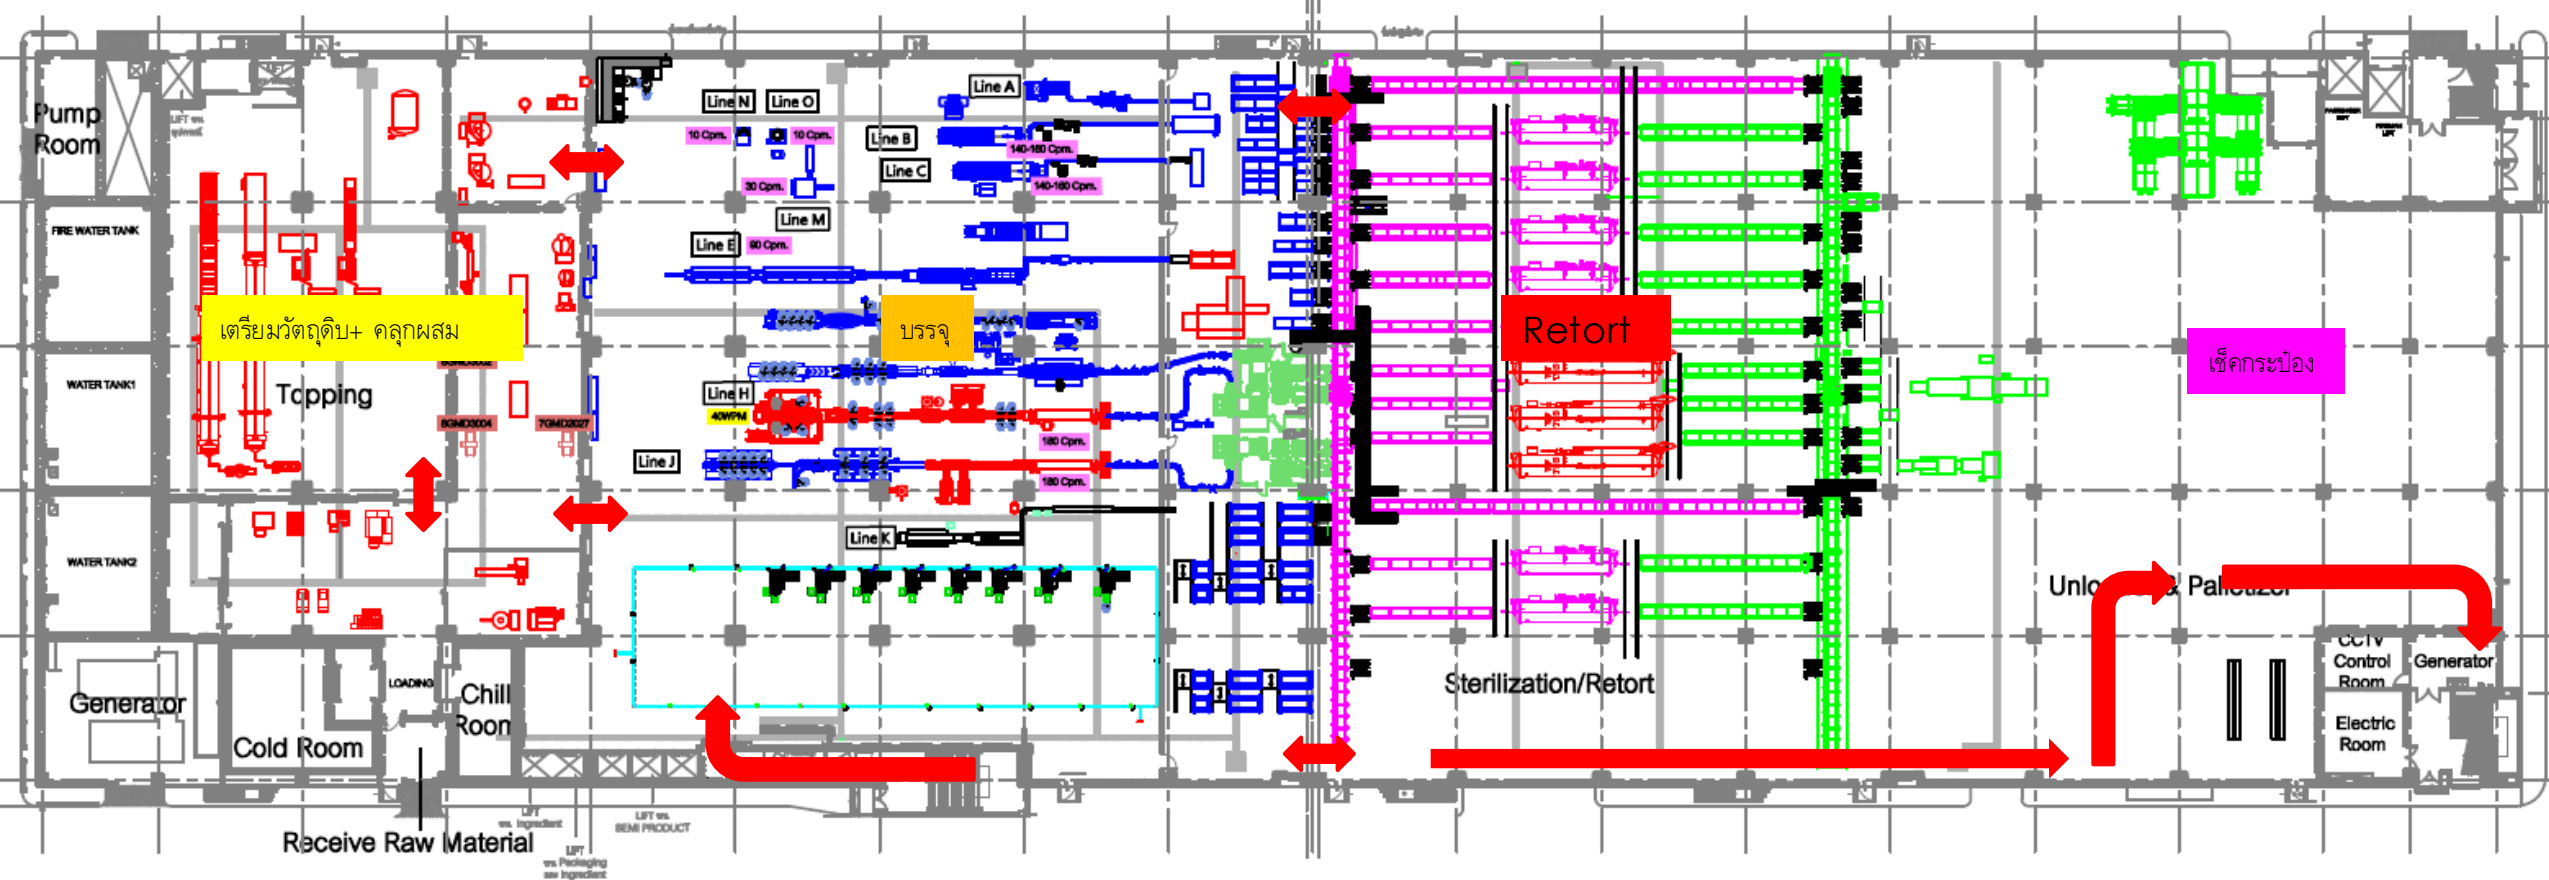

Zone 6 พื้นที่การผลิต ITC 2.2 F1

เตรียมวัตถุดิบ+ คลุกผสม


บรรจุ

Retort

เชื้อกระป๋อง

ZONE 7

พื้นที่ส่วนกลางITC 2.2 F1.5

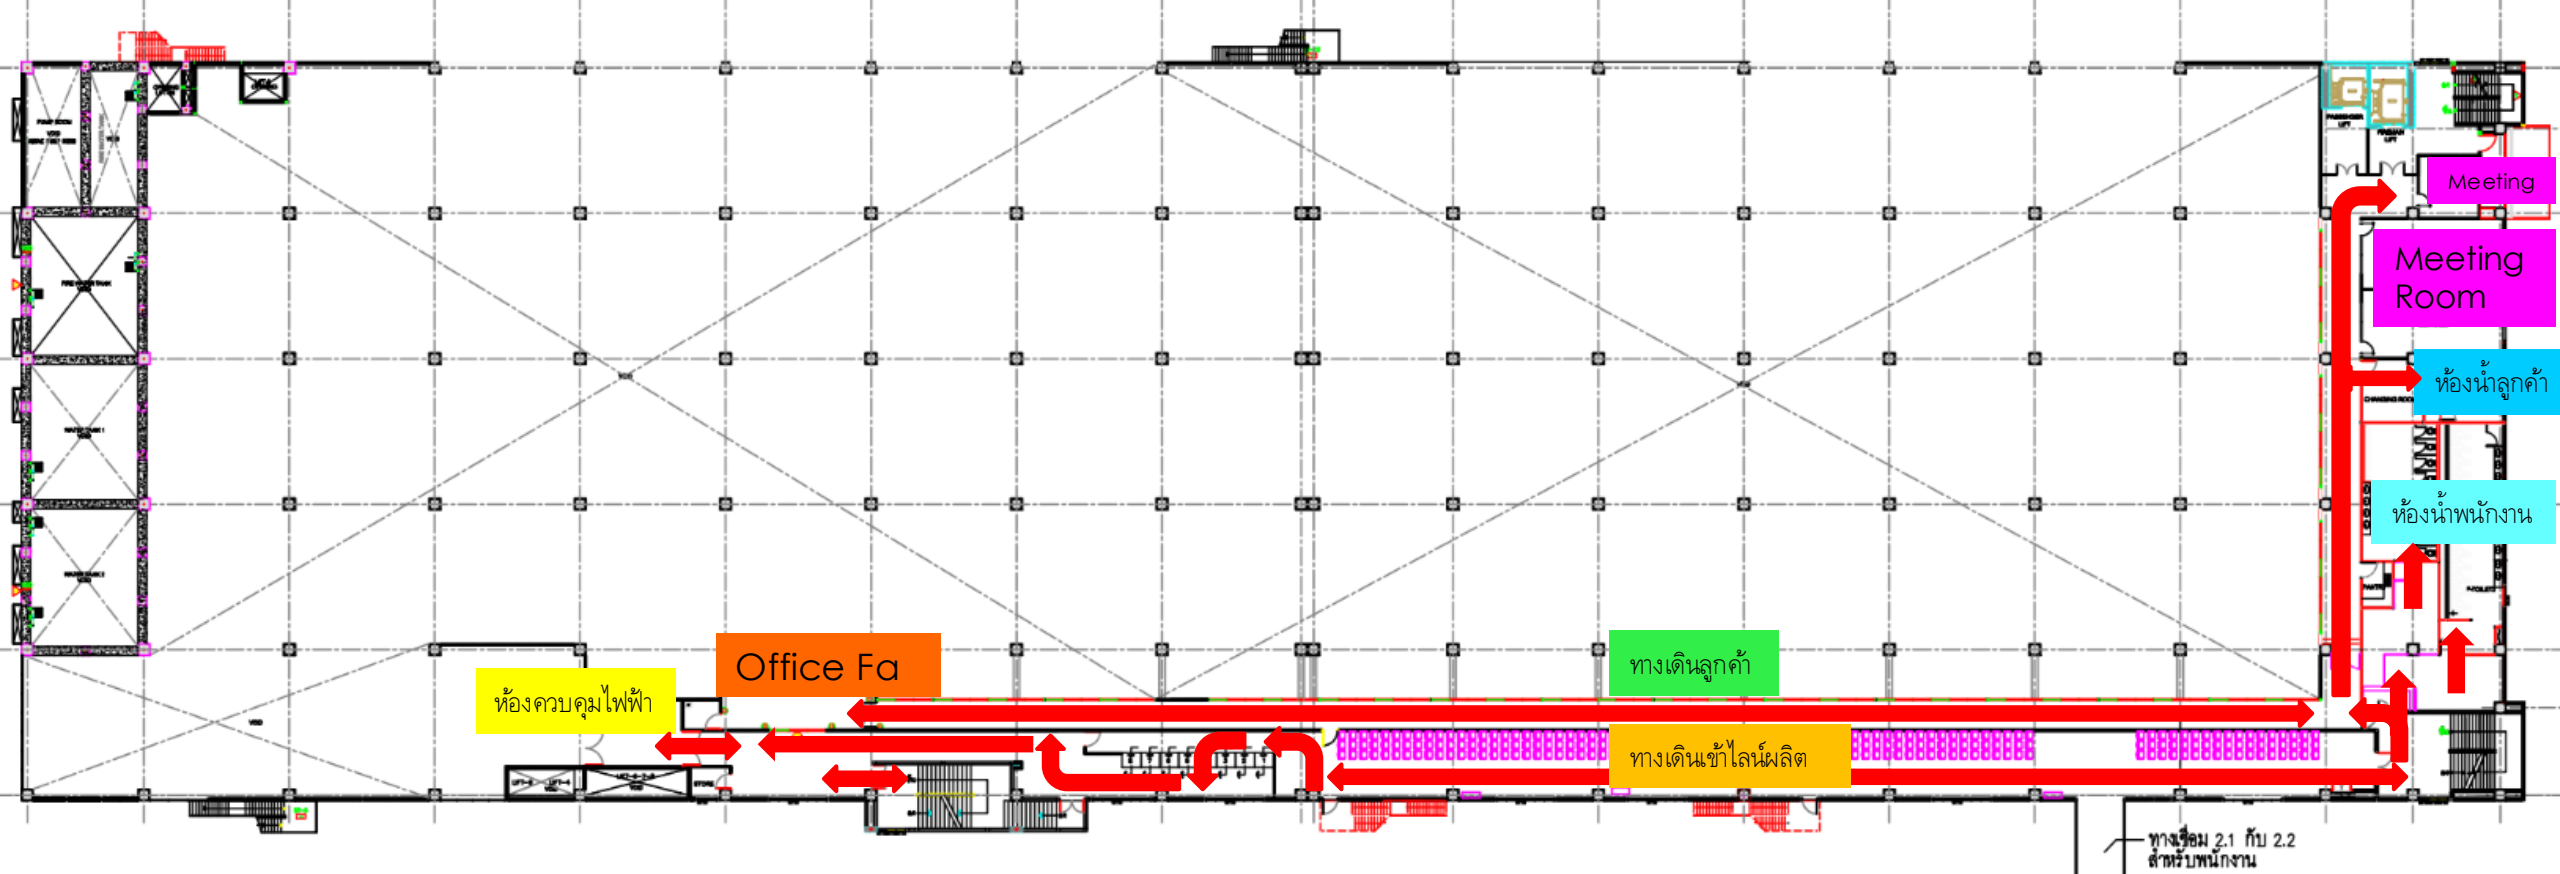

MEZZANIE 1 FLOOR PLAN

Zone 7 พื้นที่ส่วนกลาง ITC 2.2 F1.5

ห้องควบคุมไฟฟ้า

ห้องน้ำลูกค้า

ทางเดินเข้าไลน์ผลิต

Meeting Room


ทางเดินลูกค้า

Office Fa

ห้องน้ำพนักงาน

ZONE 8

พื้นที่การผลิต ITC 2.2 F2

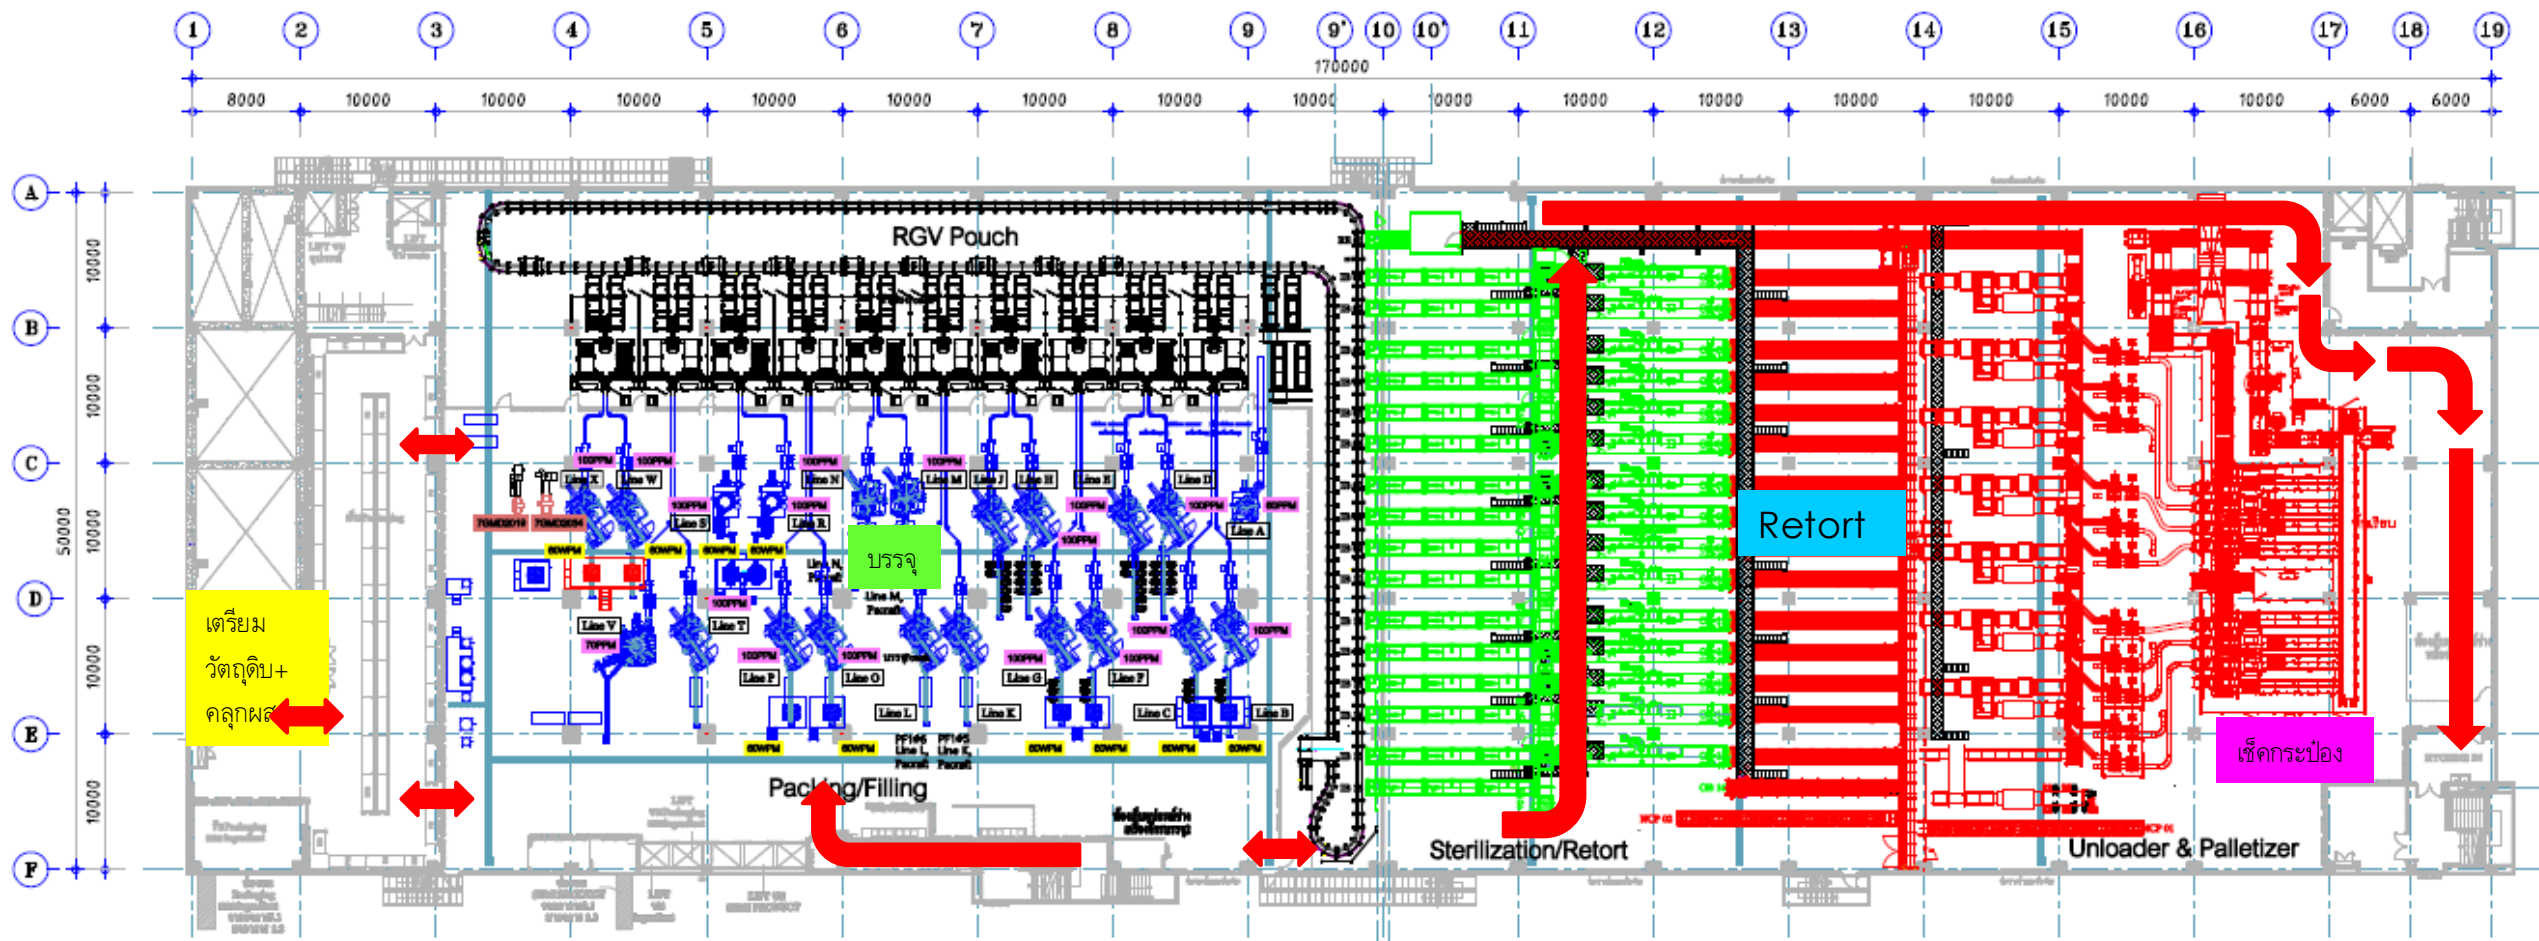

Zone 8 พื้นที่การผลิต ITC 2.2 F2

เตรียมวัตถุดิบ+ คลุกผสม


เช็ดกระป๋อง

บรรจุ

Retort

ZONE 9

พื้นที่ส่วนกลาง ITC 2.2 F2.5

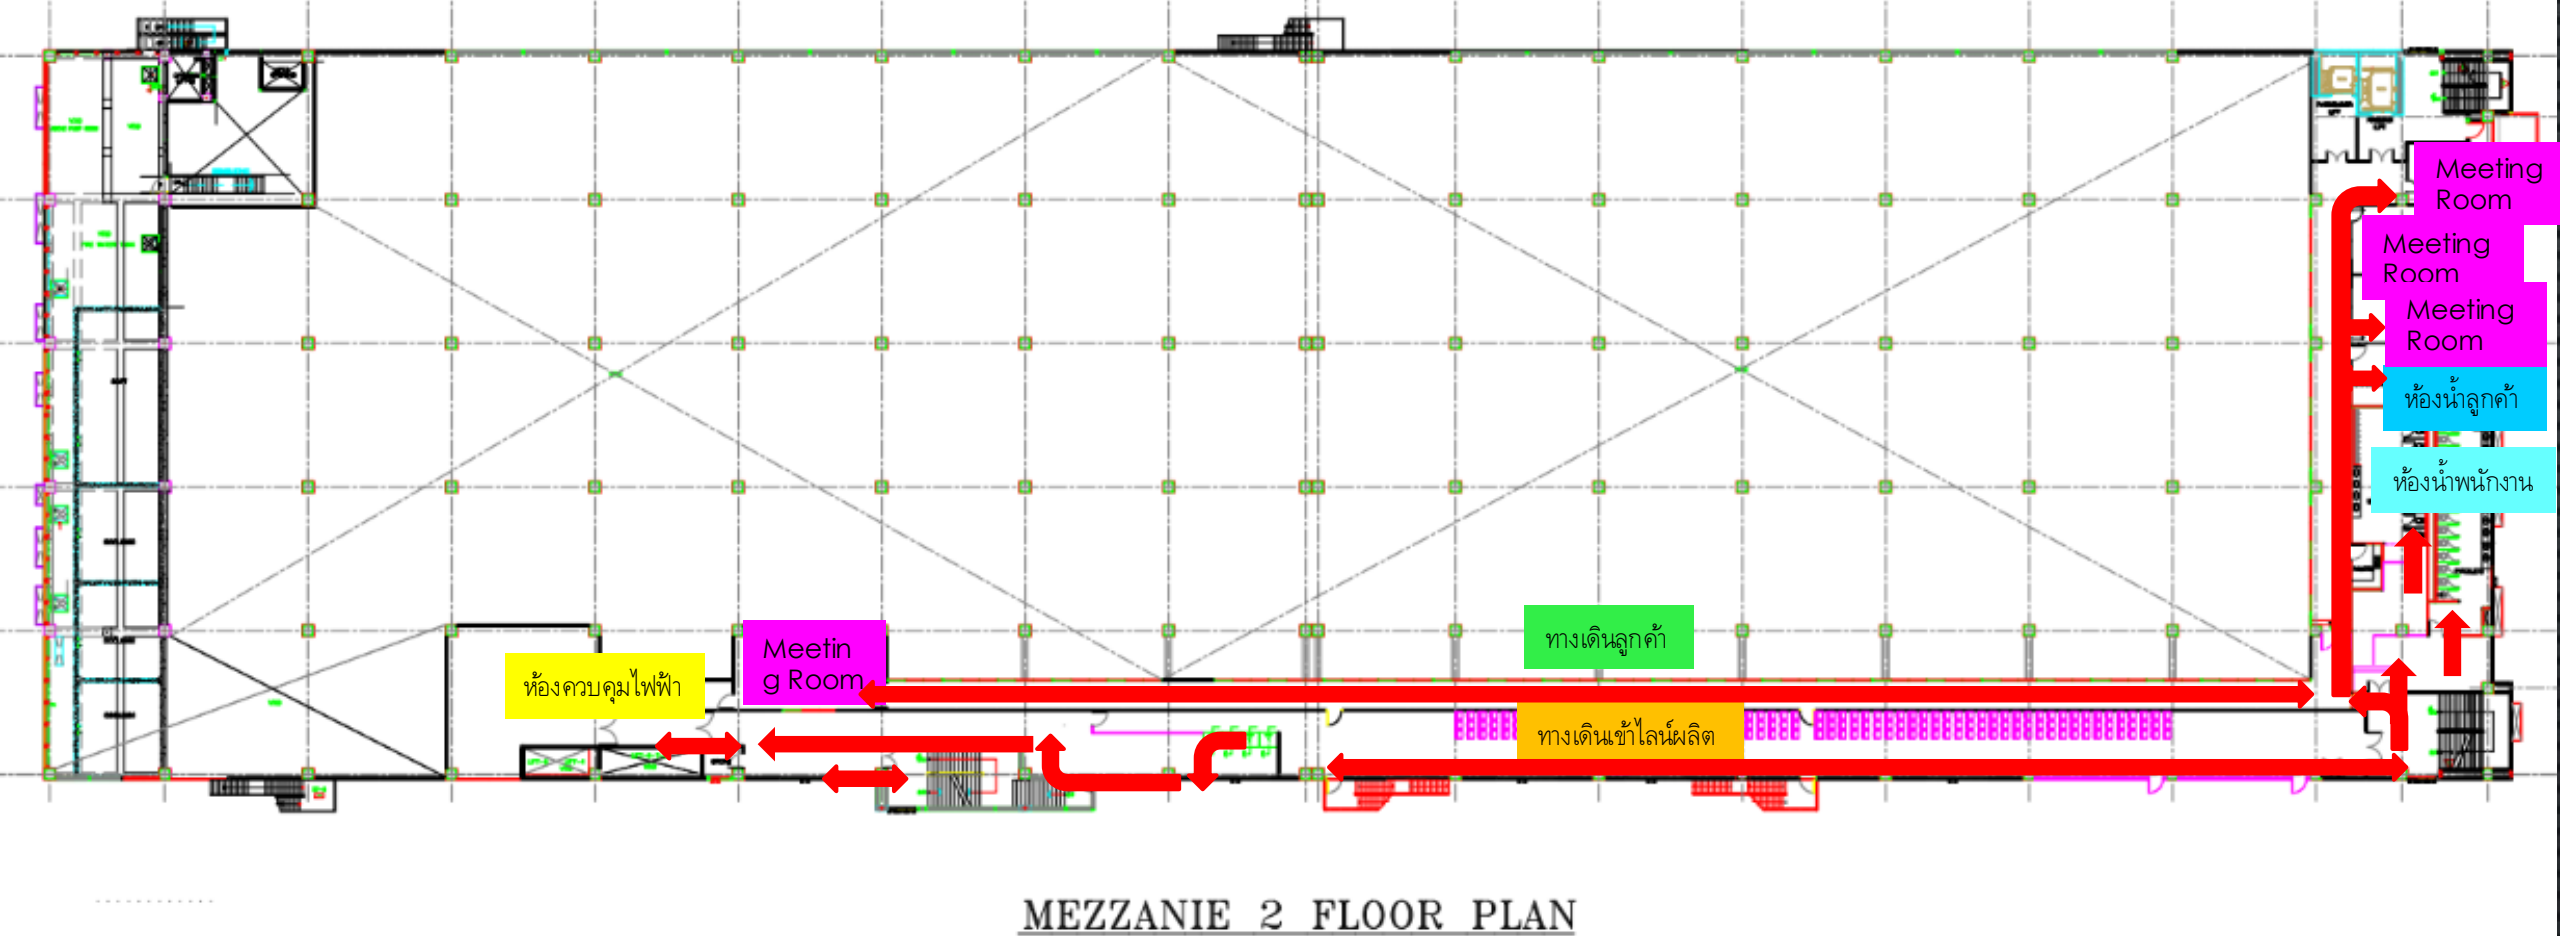

Zone 9 พื้นที่ส่วนกลาง ITC 2.2 F2.5

ห้องควบคุมไฟฟ้า

ห้องน้ำลูกค้า

ทางเดินเข้าไลน์ผลิต


Meeting Room

ทางเดินลูกค้า

ห้องน้ำพนักงาน

ZONE 10

พื้นที่การผลิต ITC 2.2 F3

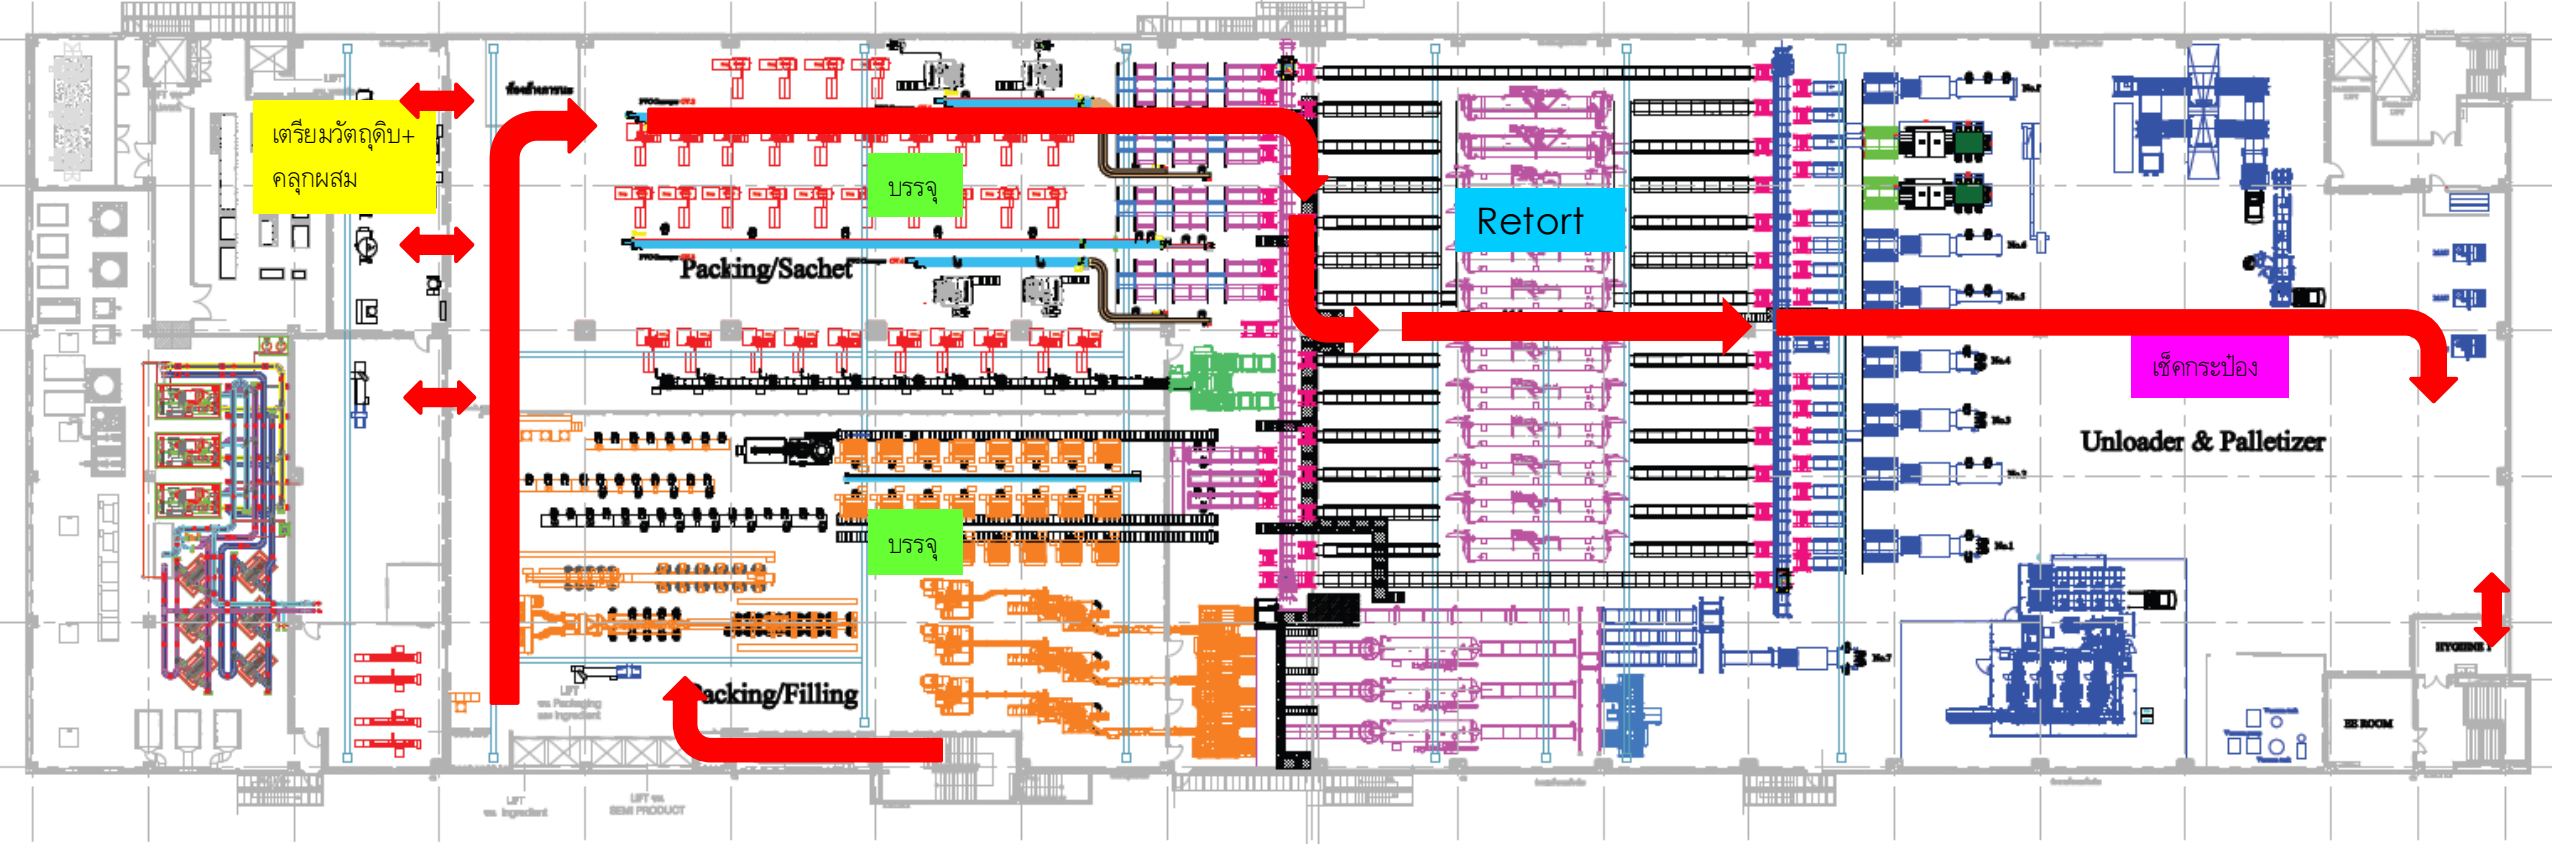

Zone 10 พื้นที่การผลิต ITC 2.2 F3

เตรียมวัตถุดิบ+ คลุกผสม

บรรจุ

Retort

เช็กระบอง

ZONE 11

พื้นที่ปิดฉลาก 40 ไร่ ITC 2

อาคารผลิต 2.2

พื้นที่ 26,800.00²m

กว้าง 50.0 m ยาว 180.0 m

11

ถนนโครงการ

Zone 11 พื้นที่ปิดฉาก 40 ไร่ ITC 2.2 F2

ไลน์ปิดฉาก

ลานโหลด

ห้องเย็น C

สโตร์

ถนนโครงการ

ไลน์ปิดฉาก

14

Warehouse

พื้นที่ 3,685.00 m²

กว้าง 57.00 m ยาว 64.50 m

Cold Storage 2

พื้นที่ 3,665.00 m²

กว้าง 55.00 m ยาว 71.00 m

15

16

LOAD

พื้นที่

ลานโหลด

กว้าง 19.50 m ยาว 56.50 m

17

Cold Storage

พื้นที่ 625.00 m²

กว้าง 17.00 m ยาว 36.50 m

ห้องเย็น C

สโตร์

ที่โล่ง

< 65.071 ->

< 77.631 ->

ทางออกถนนโครงการ

ถนนร่วมส่วนมคค 8.00 ม.


< 61.293 ->

ZONE 12

พื้นที่ห้องเย็น ITC 2

Zone 12 ห้องเย็น ITC2

พื้นที่ห้องเย็น / จุดลงปลา คัดปลา

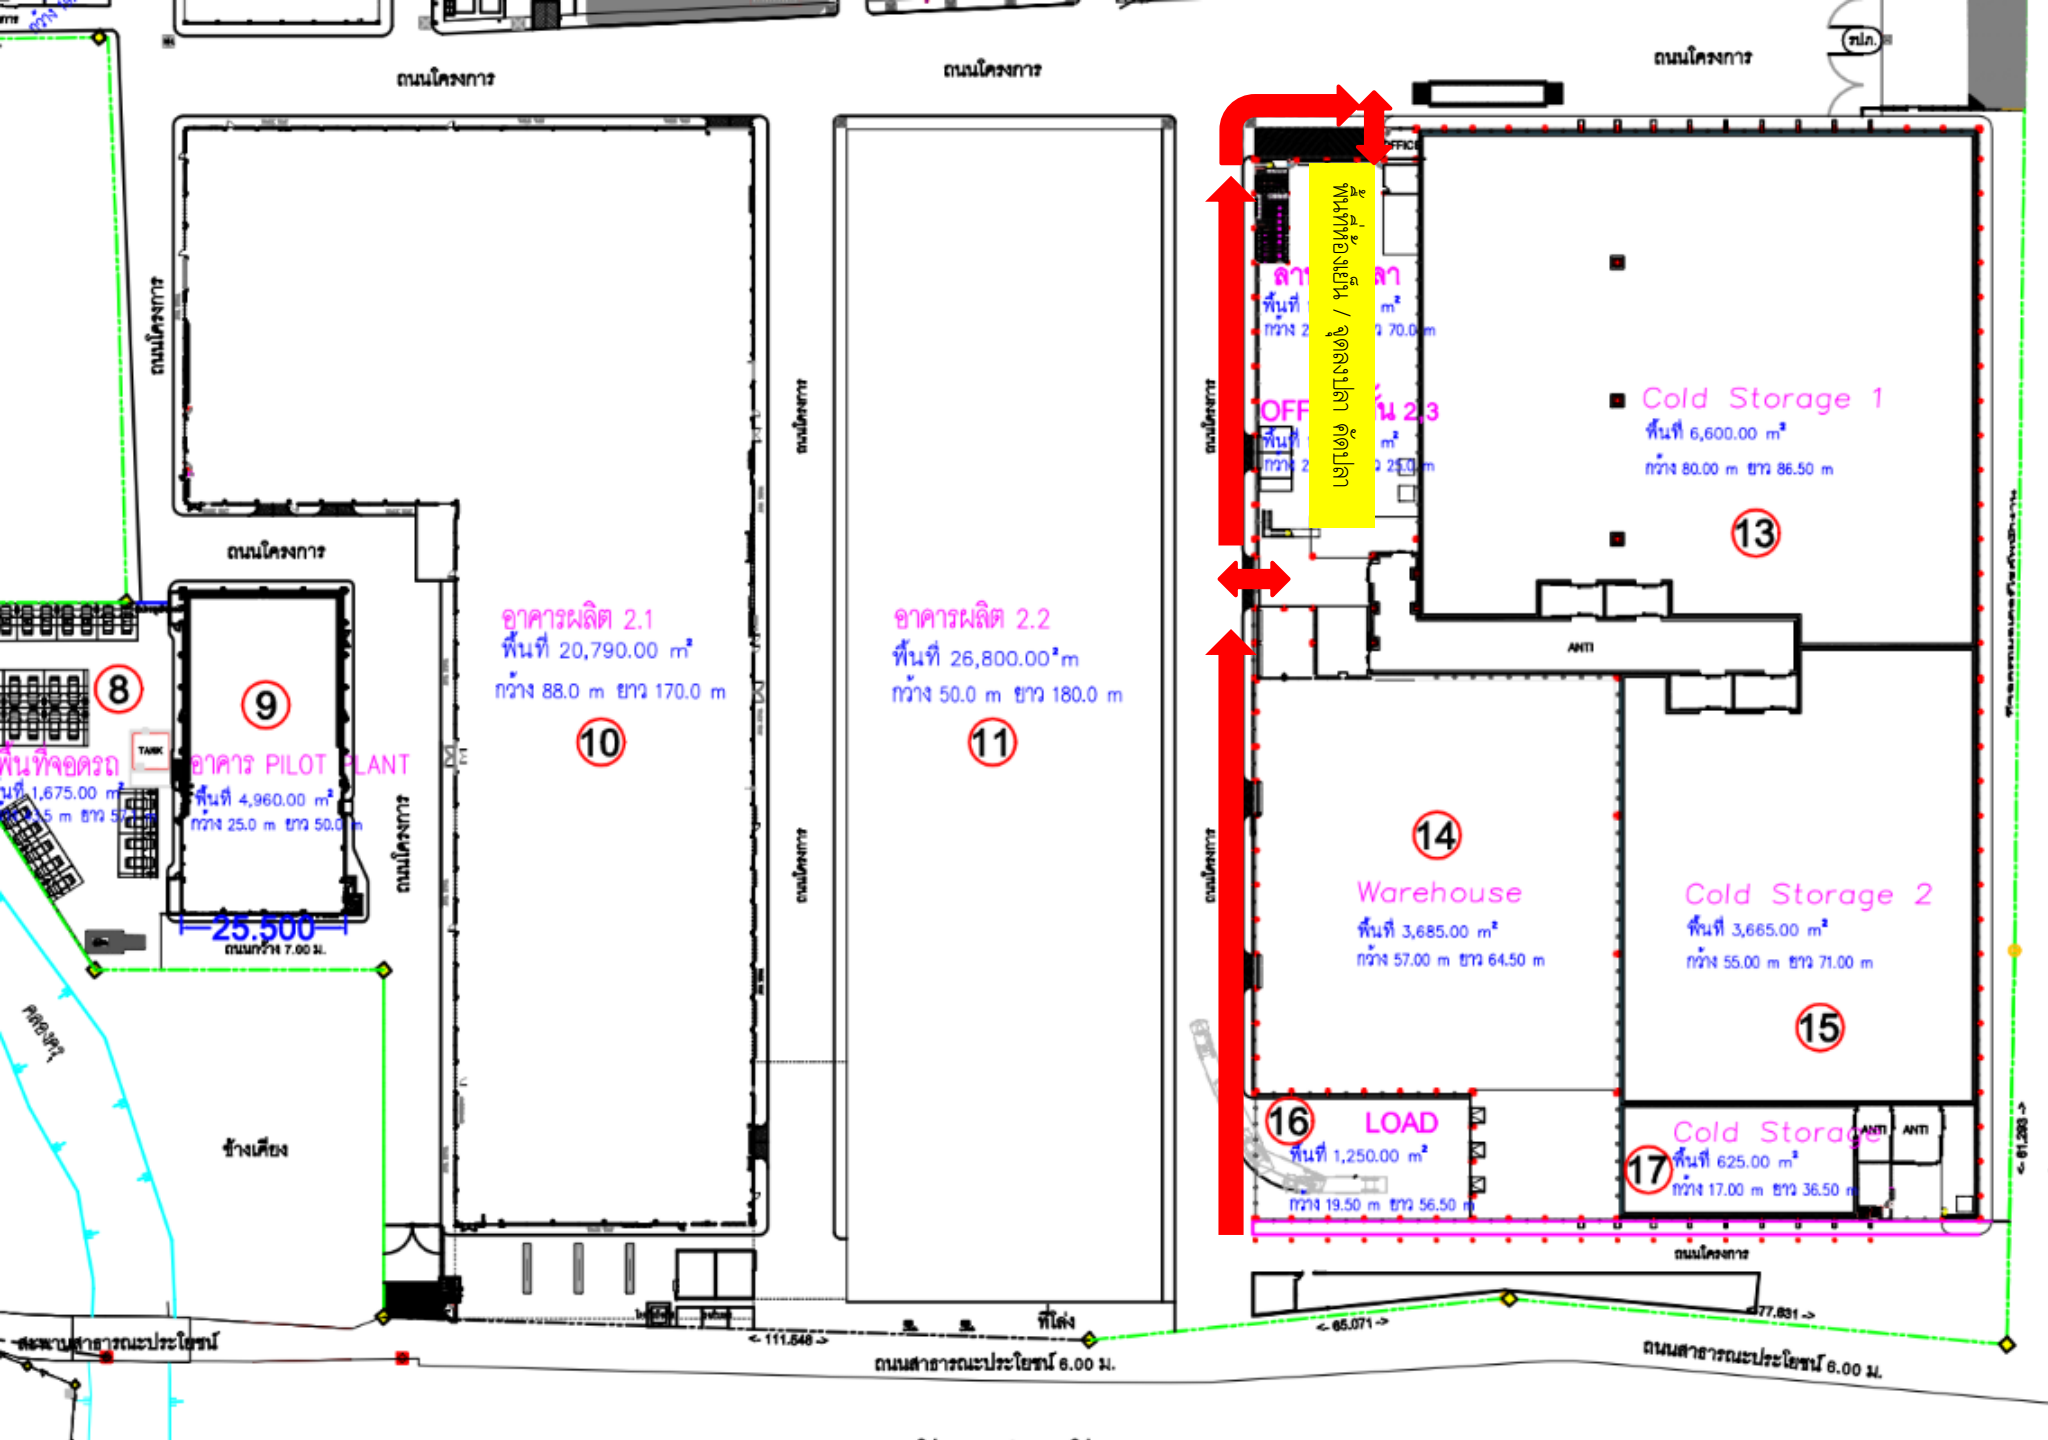

ZONE 13

พื้นที่รอบนอก ITC 2

Zone 13 พื้นที่รอบนอก ITC2

ข้อ ๑

รอบอาคาร ITC 2.1

ข้อ 2

รอบอาคาร ITC 2.2

จุดเก็บถังปลา

รอบอาคาร ห้องเย็น / 40 ไร่

Boiler

ห้องขยะ

ลานจอดรถ

หมายเลขอาคาร	รายละเอียดของอาคาร/ใช้โรงงาน	ขนาดของอาคาร	พื้นที่ใช้สอย
อาคาร 1	พื้นที่ประกอบชิ้น ชะนิบิล ชื่นเดียว	กว้าง 10.00ม ยาว 14.00ม	140.00 m ²
อาคาร 2	อาคารเก็บเครื่องจักร ชื่นเดียว	กว้าง 10.00ม ยาว 70.00ม	700.00 m ²
อาคาร 3	อาคารร้านค้าเครื่องจักร MC SHOP ชั้น 1,2	กว้าง 16.00ม ยาว 22.50ม	180.00 m ²
	ส่วน OFFICE ชั้น 2	กว้าง 4.50ม ยาว 12.00ม	55.00 m ²
อาคาร 4	อาคาร SMOKE ชั้นเดียว	กว้าง 19.00ม ยาว 20.00ม	465.50 m ²
อาคาร 5	อาคาร BOILER ชั้นเดียว	กว้าง 30.00ม ยาว 37.00ม	950.00 m ²
อาคาร 6	ที่ปิดน้ำมันดิบ ส่วน OFFICE 2 ชั้น	กว้าง 57.50ม ยาว 60.00ม	3,450.00 m ²
อาคาร 7	พื้นที่วางถังปลา ชั้นเดียว	กว้าง 33.50ม ยาว 62.00ม	2,077.50 m ²
อาคาร 8	พื้นที่จอดรถ ชั้นเดียว	กว้าง 43.50ม ยาว 57.00ม	1,677.00 m ²
อาคาร 9	อาคาร PILOT PLANT 5 ชั้น	กว้าง 25.00ม ยาว 50.00ม	1,250.00 m ²
อาคาร 10	อาคารผลิต 2.1 2 ชั้น	กว้าง 88.50ม ยาว 170.50ม	20,790.00 m ²
อาคาร 11	อาคารผลิต 2.2 ชั้น 1,1.5,2.2.5,3	กว้าง 50.00ม ยาว 182.00ม	26,800.00 m ²
อาคาร 12	ลานปลา ชั้นเดียว	กว้าง 25.50ม ยาว 70.00ม	1,705.00 m ²
	ส่วน OFFICE ชั้น 2,3	กว้าง 21.50ม ยาว 25.00ม	1,075.00 m ²
อาคาร 13	COLD STORAGE 1 ชั้นเดียว	กว้าง 80.00ม ยาว 86.50ม	6,605.00 m ²
อาคาร 14	WAREHOUSE ชั้นเดียว	กว้าง 57.00ม ยาว 64.50ม	3,685.00 m ²
อาคาร 15	COLD STORAGE 2 ชั้นเดียว	กว้าง 55.00ม ยาว 71.00ม	3,665.00 m ²
อาคาร 16	ที่จอดรถ LOAD ชั้นเดียว	กว้าง 19.50ม ยาว 56.50ม	1,125.00 m ²
อาคาร 17	COLD STORAGE ชั้นเดียว	กว้าง 17.00ม ยาว 36.50ม	625.00 m ²
อาคาร 18	อาคารเก็บขนปลา ชั้นเดียว	กว้าง 6.00ม ยาว 35.50ม	240.00 m ²
รวมพื้นที่ใช้สอยในอาคาร 18 อาคารทั้งหมด			77,260.00 m ²



ผังบริเวณ - พื้นที่ใช้สอยภายในอาคาร 1-TAL2.

มาตราส่วน 1:2000